


development drawings

apartment - kedungu

25 january 2020

moka studio

design and build

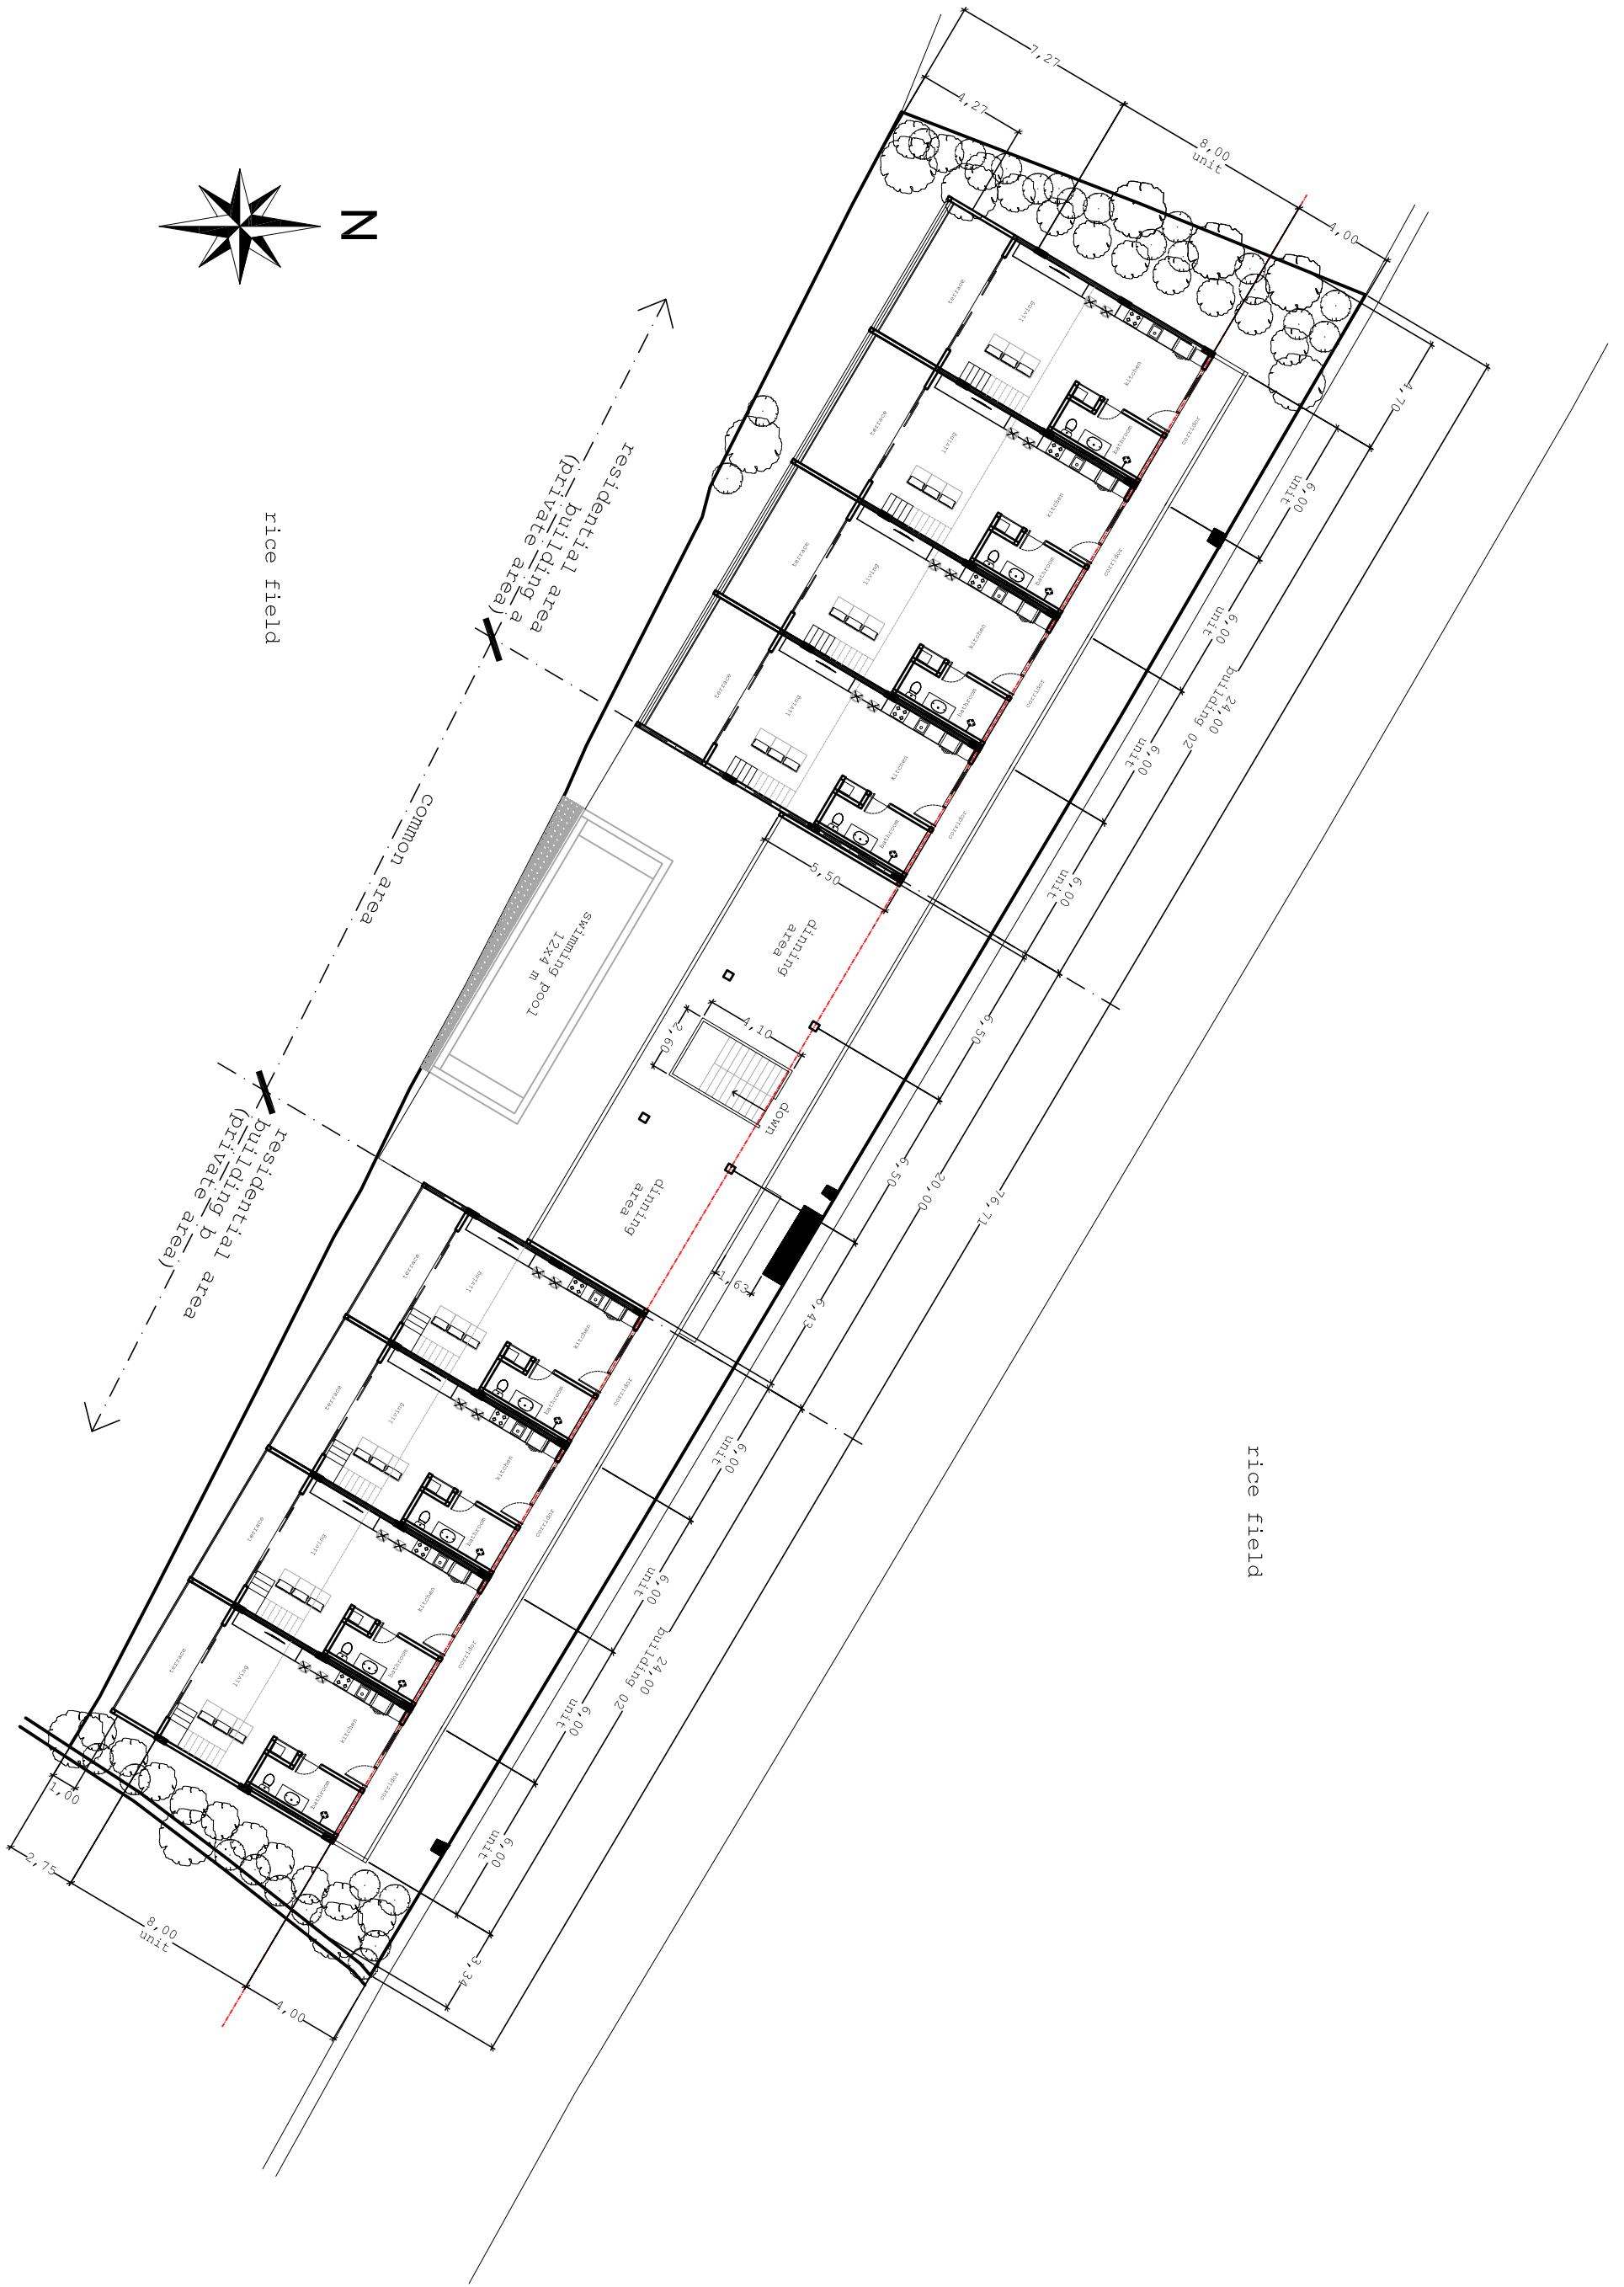

contractors must check all dimensions on site before starting any work or shop drawings.
figured dimensions to take precedence over scale readings.

this drawing is copyright and property of the architects

project title	apartment
client	mr. paul
category	development drawing
scale	A3 - 1:250
date	25 january 2021
drawing title	lay out plan
drawing number	A-1.1.2


moka studio

design and build

contractors must check all dimensions on site before starting any work or shop drawings.

figured dimensions to take precedence over scale readings.

this drawing is copyright and property of the architects

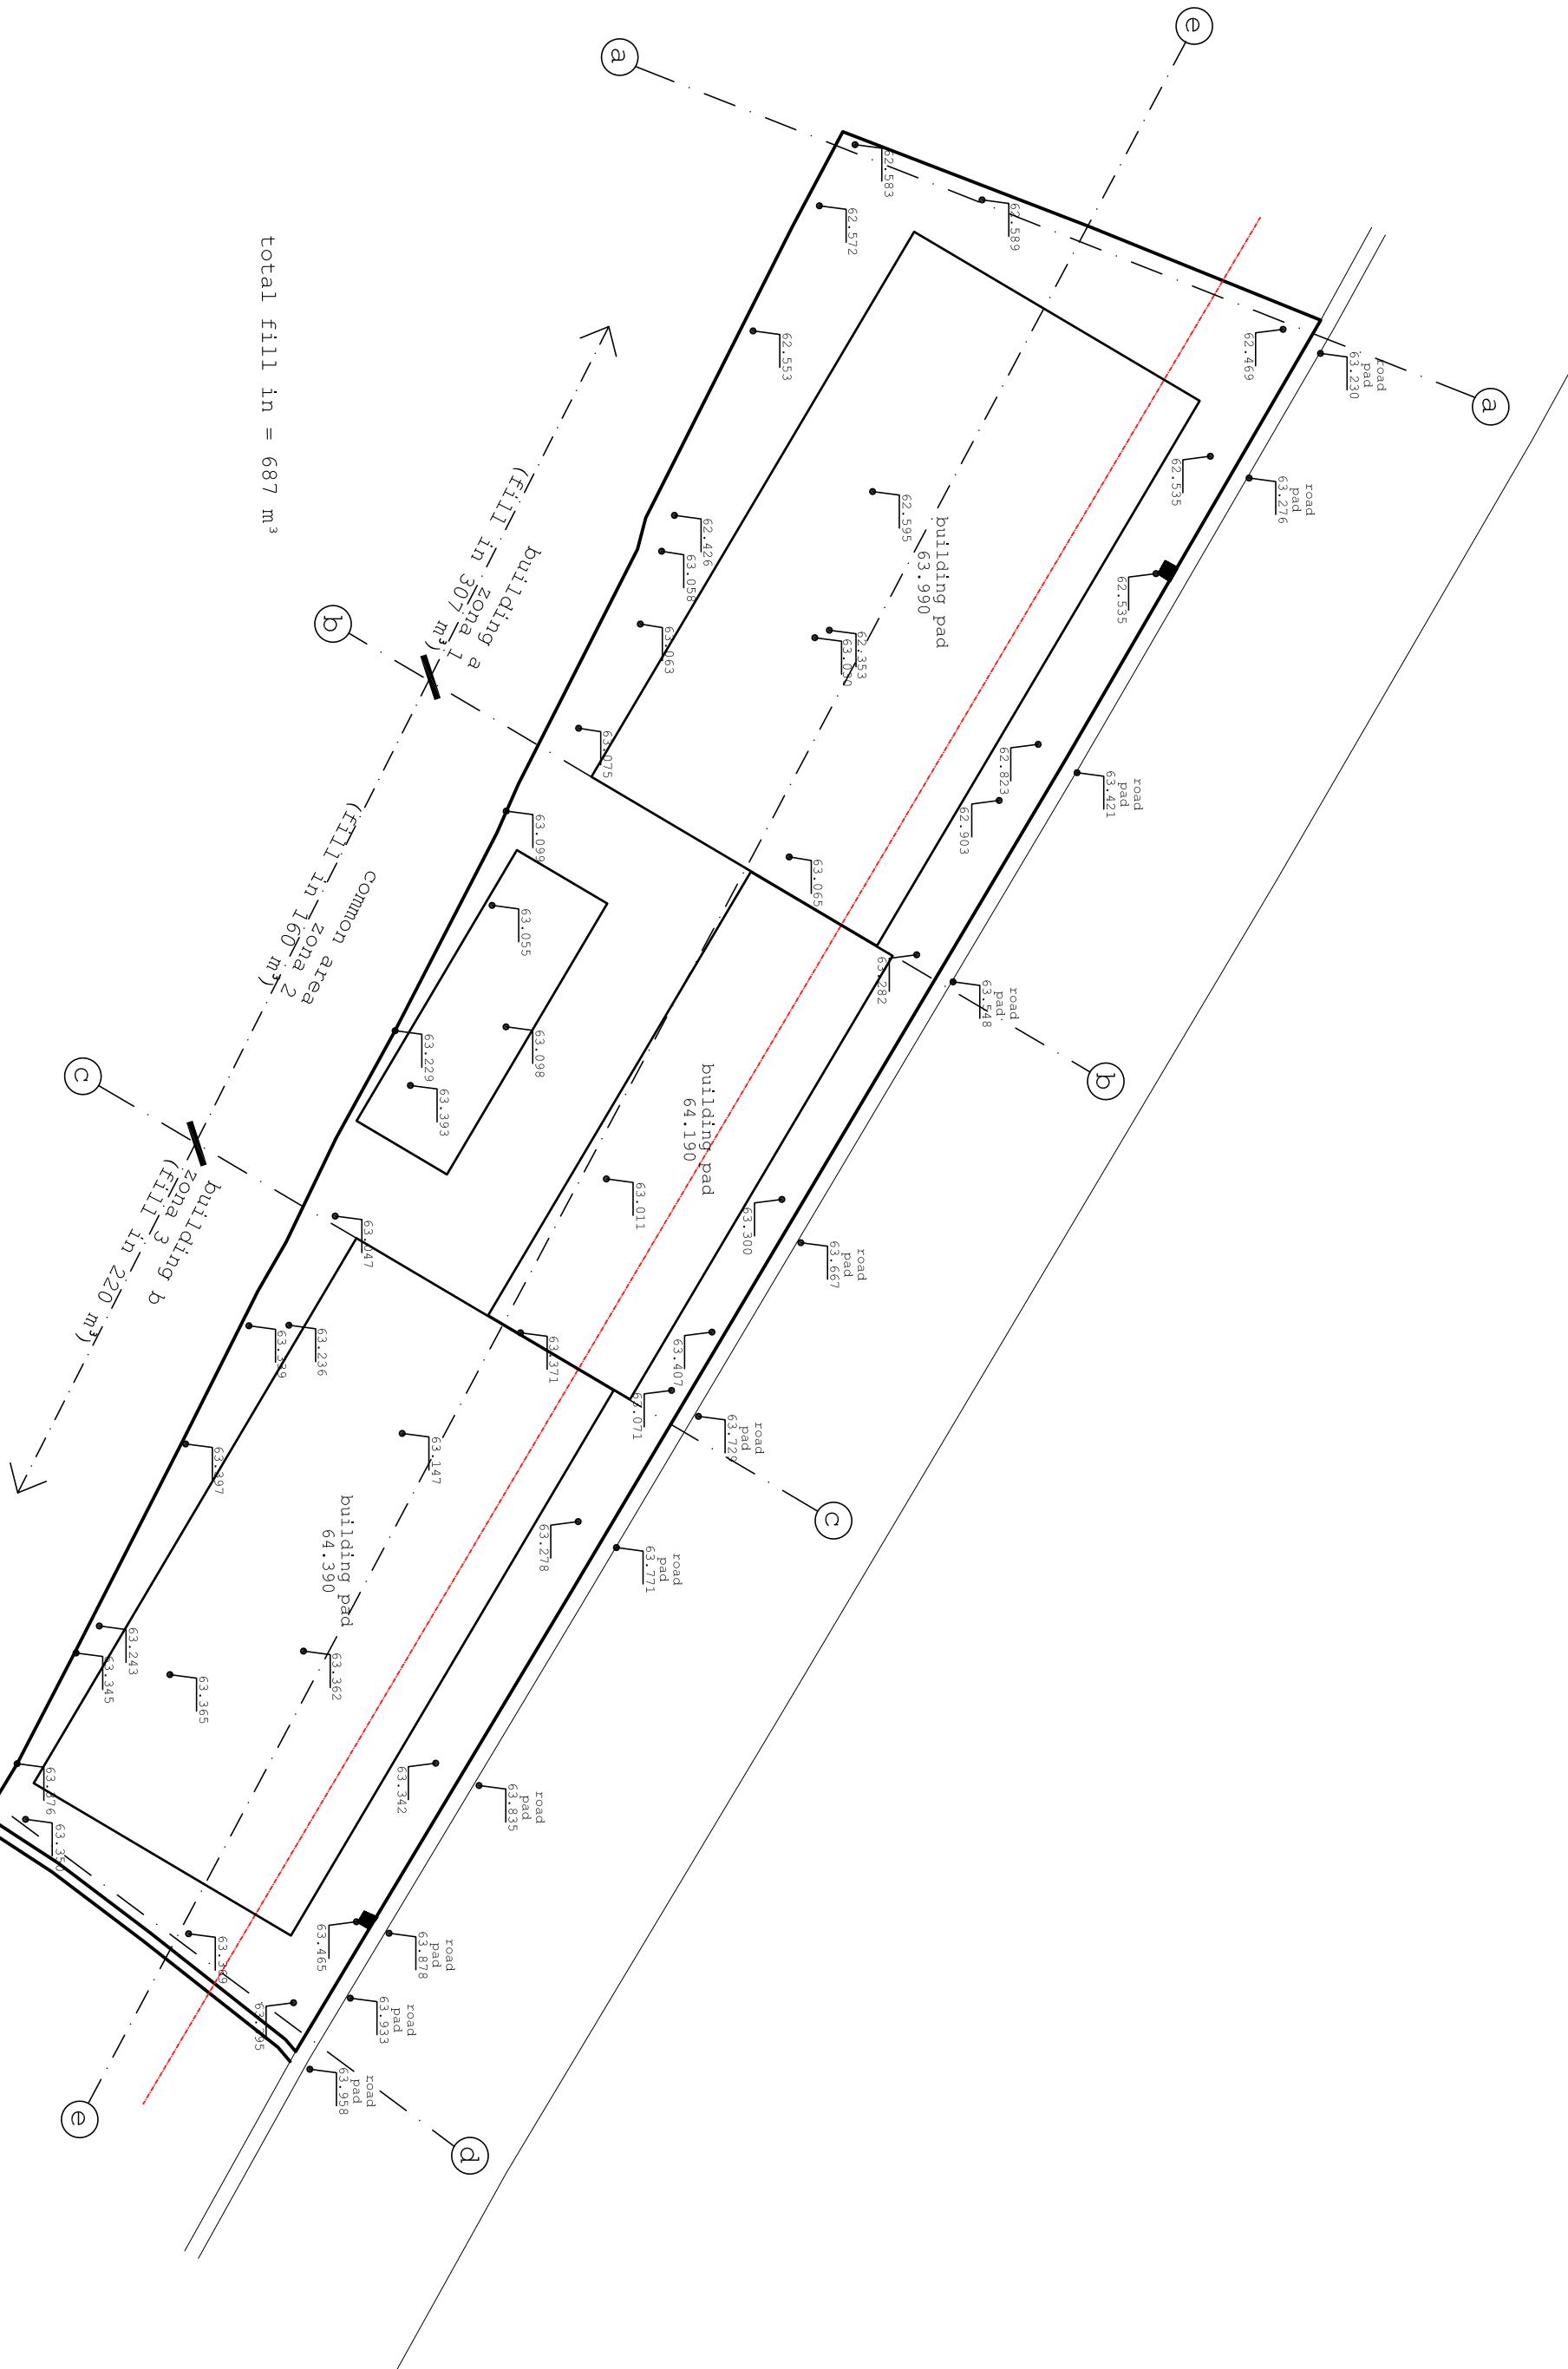

project title	checked
apartment	moka
client	mr. paul
approved	
revision	

drawing title	building pad
drawing number	A-1.1.4


contractors must check all dimensions on site before starting any work or shop drawings.

figured dimensions to take precedence over scale readings.

this drawing is copyright and property of the architects


moka studio

design and build

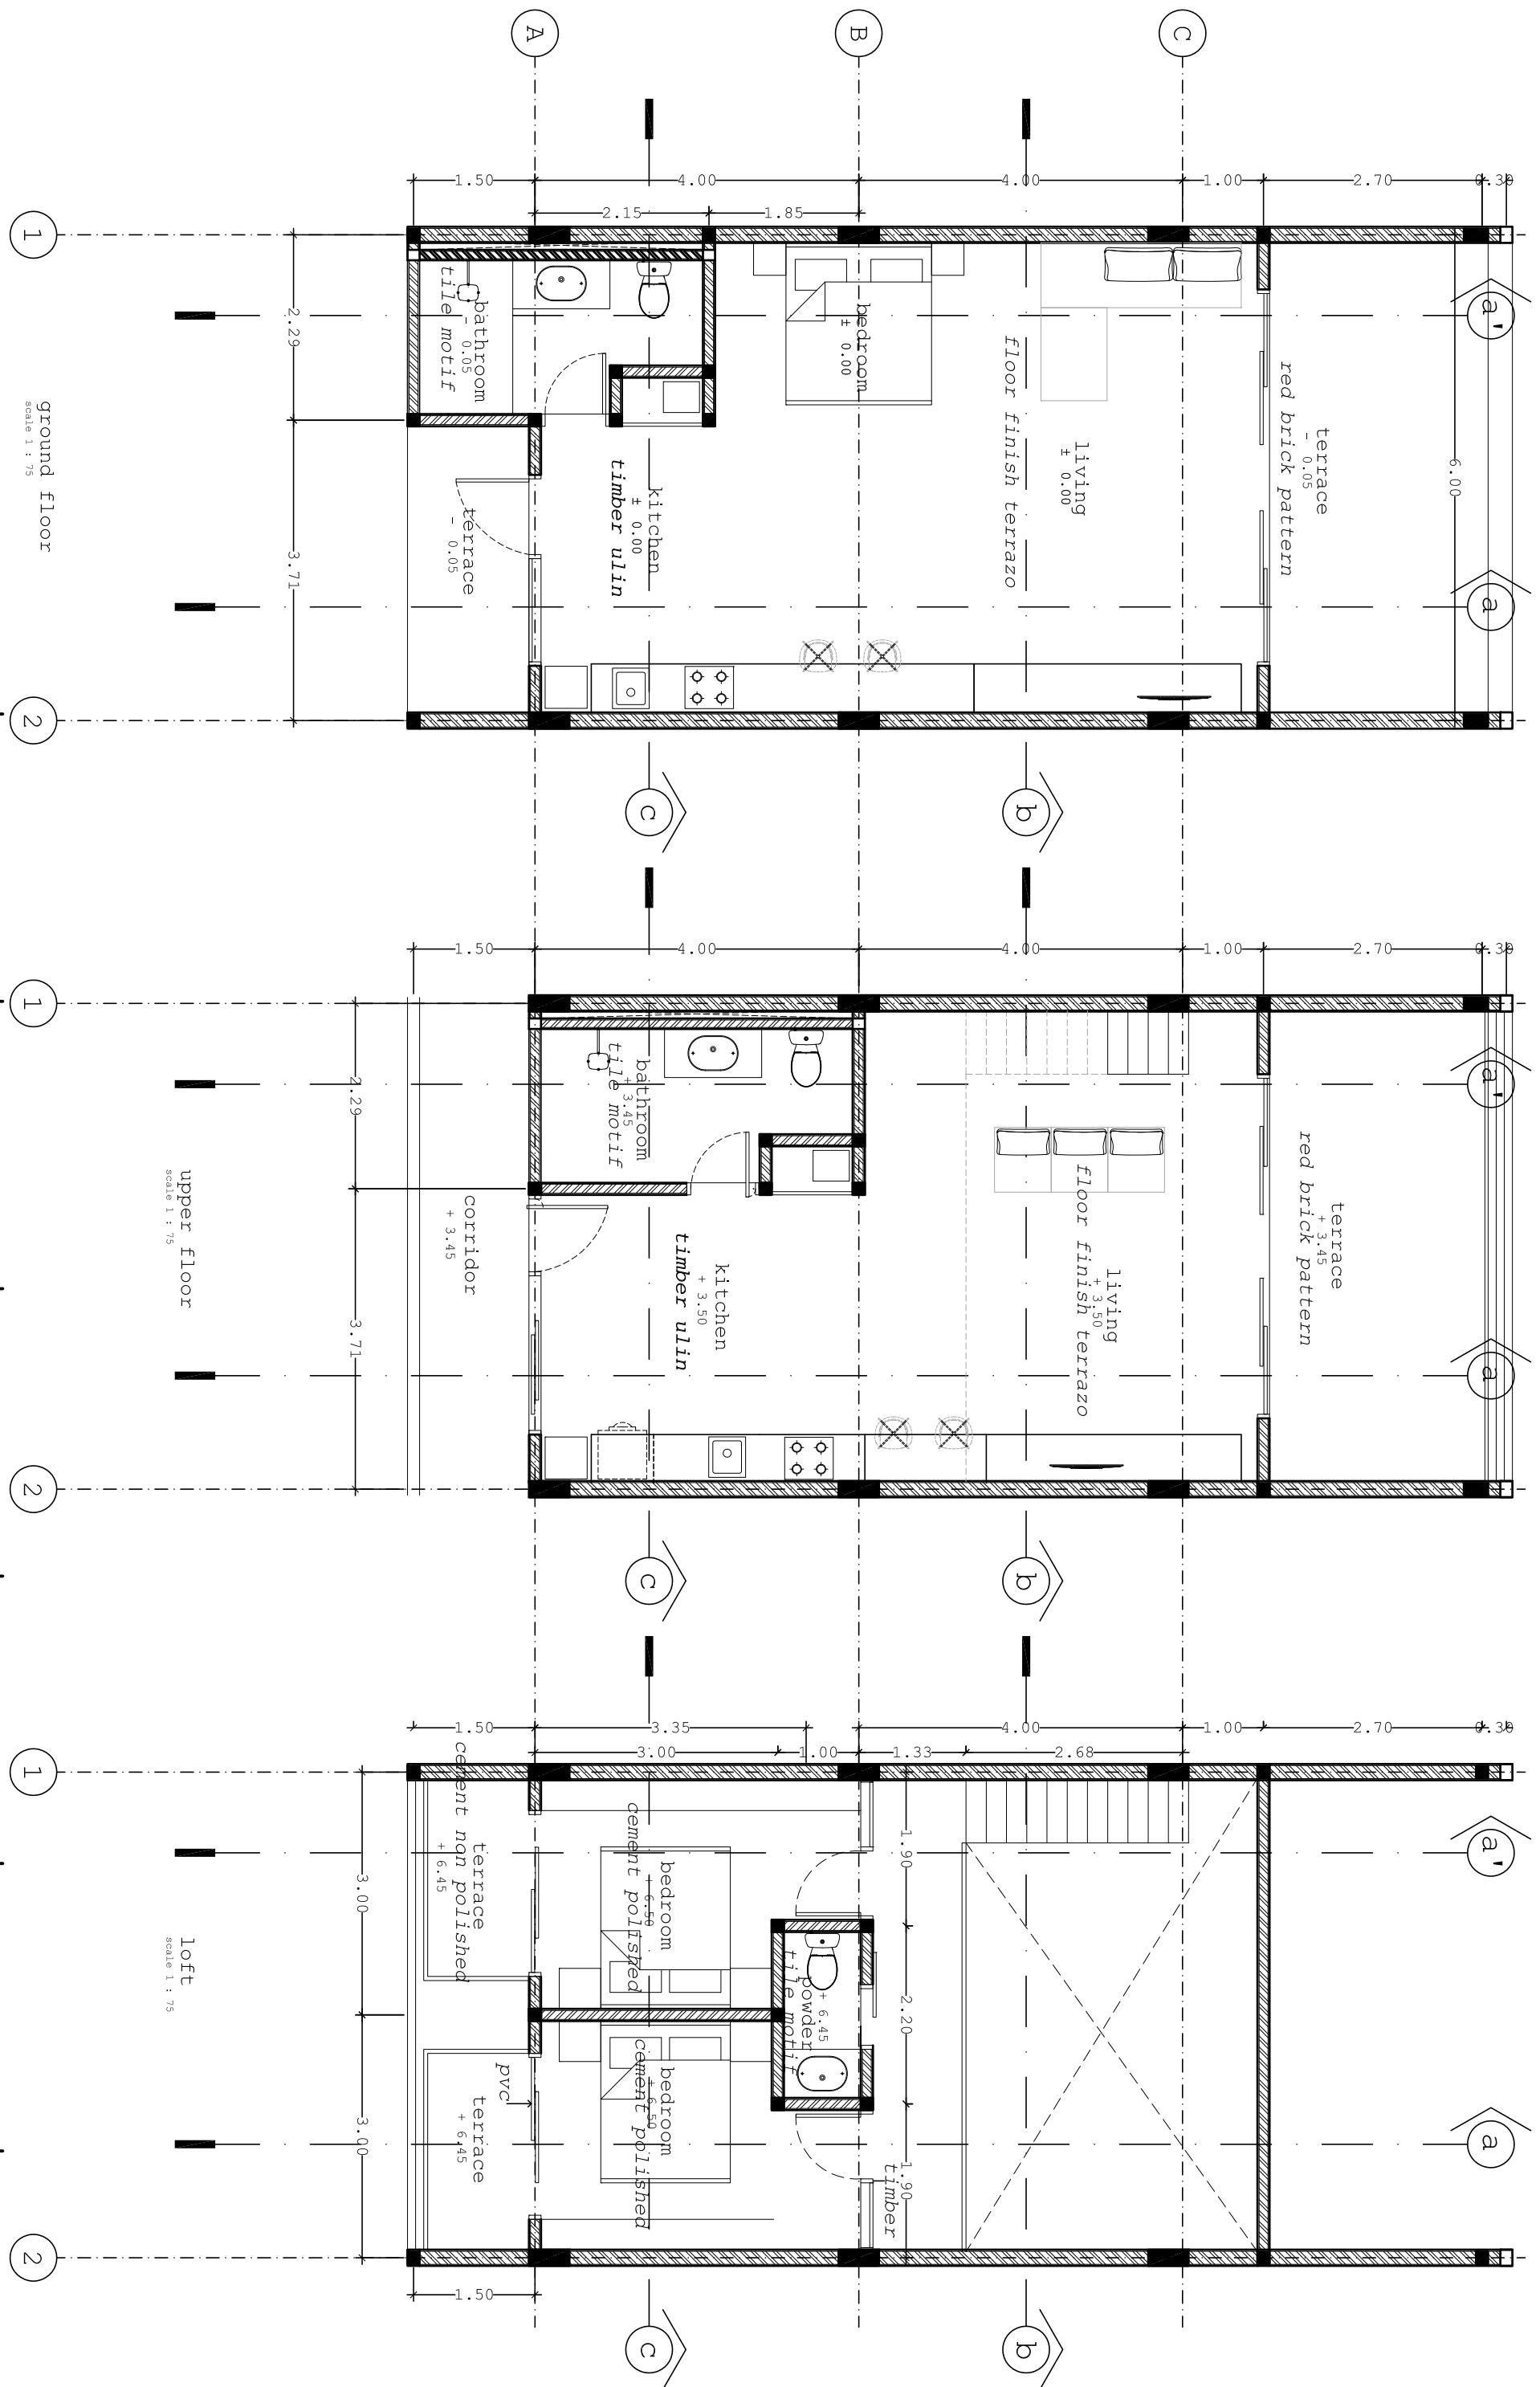

moka studio

design and build

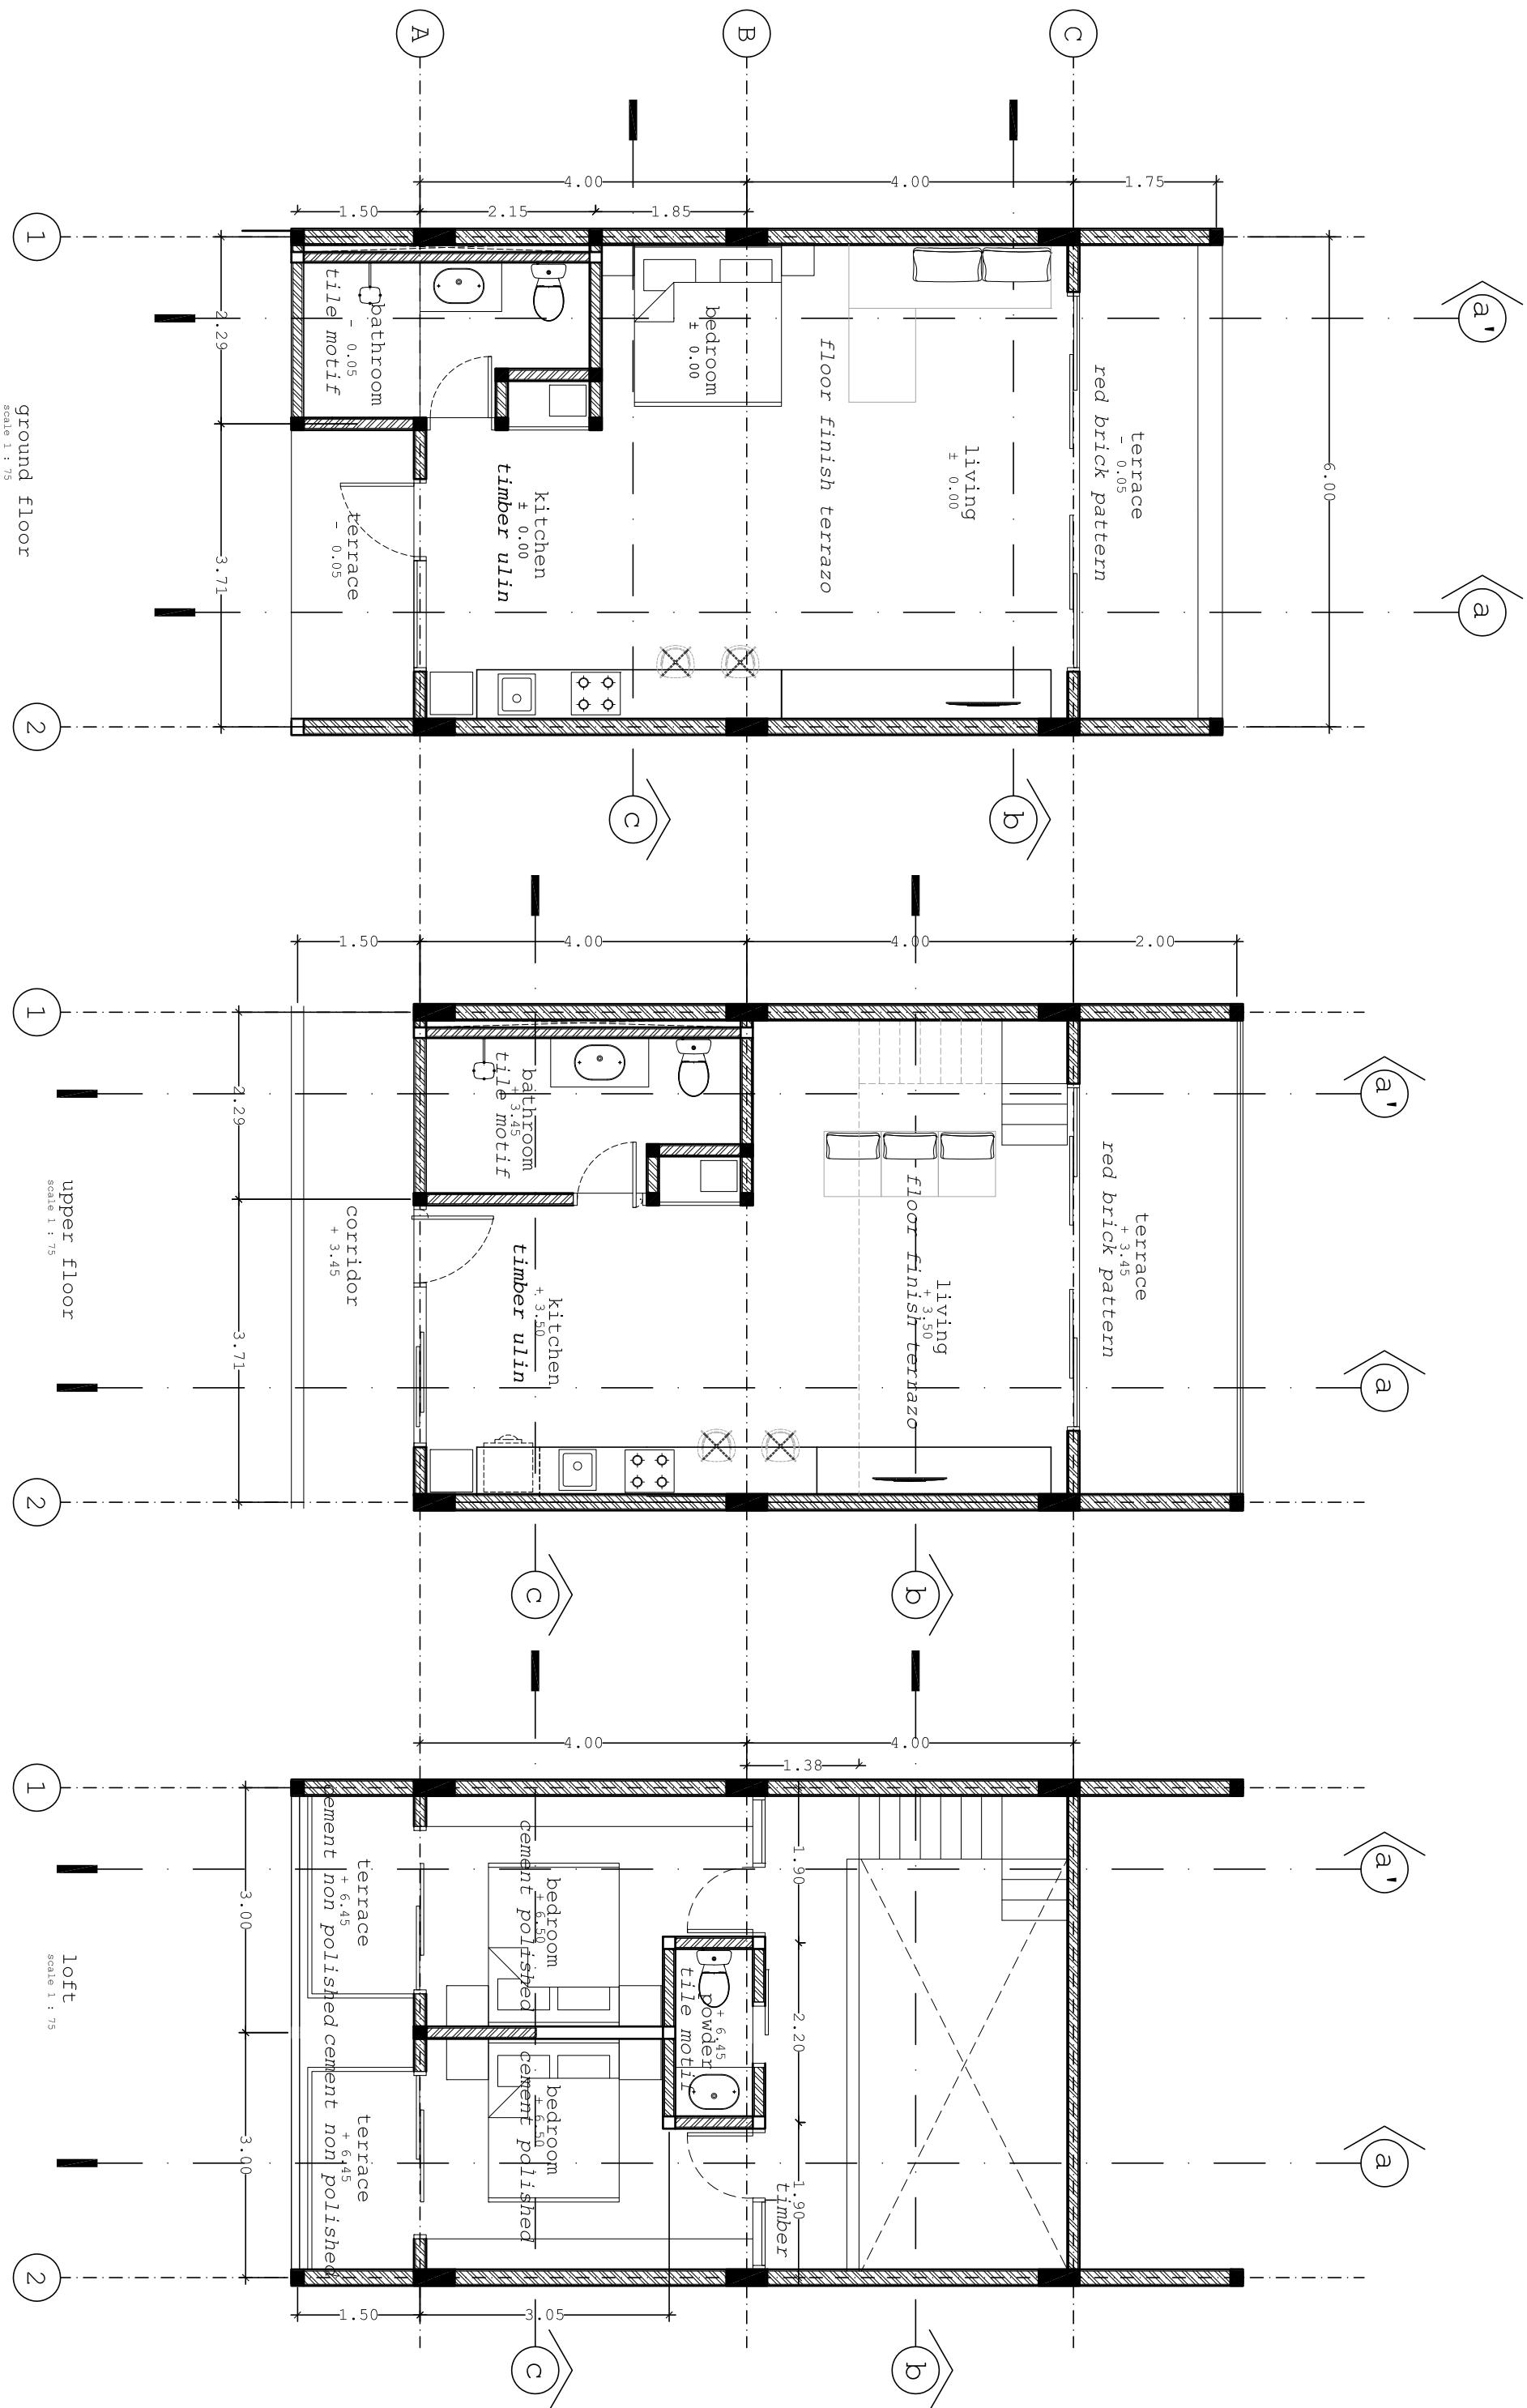

contractors must check all dimensions on site before starting any work or shop drawings.

figured dimensions to take precedence over scale readings.

this drawing is copyright and property of the architects

<u>client</u>	project <u>title</u>
mr. paul	apartment


contractors must check all dimensions on site before starting any work or shop drawings. This drawing provides dimensions to take precedence over scale readings.

<u>client</u>	apartment	<u>protect</u>
mr. paul	elite	elite

moka studio
design and build

design and build

ground floor lobby
scale 1 : 100

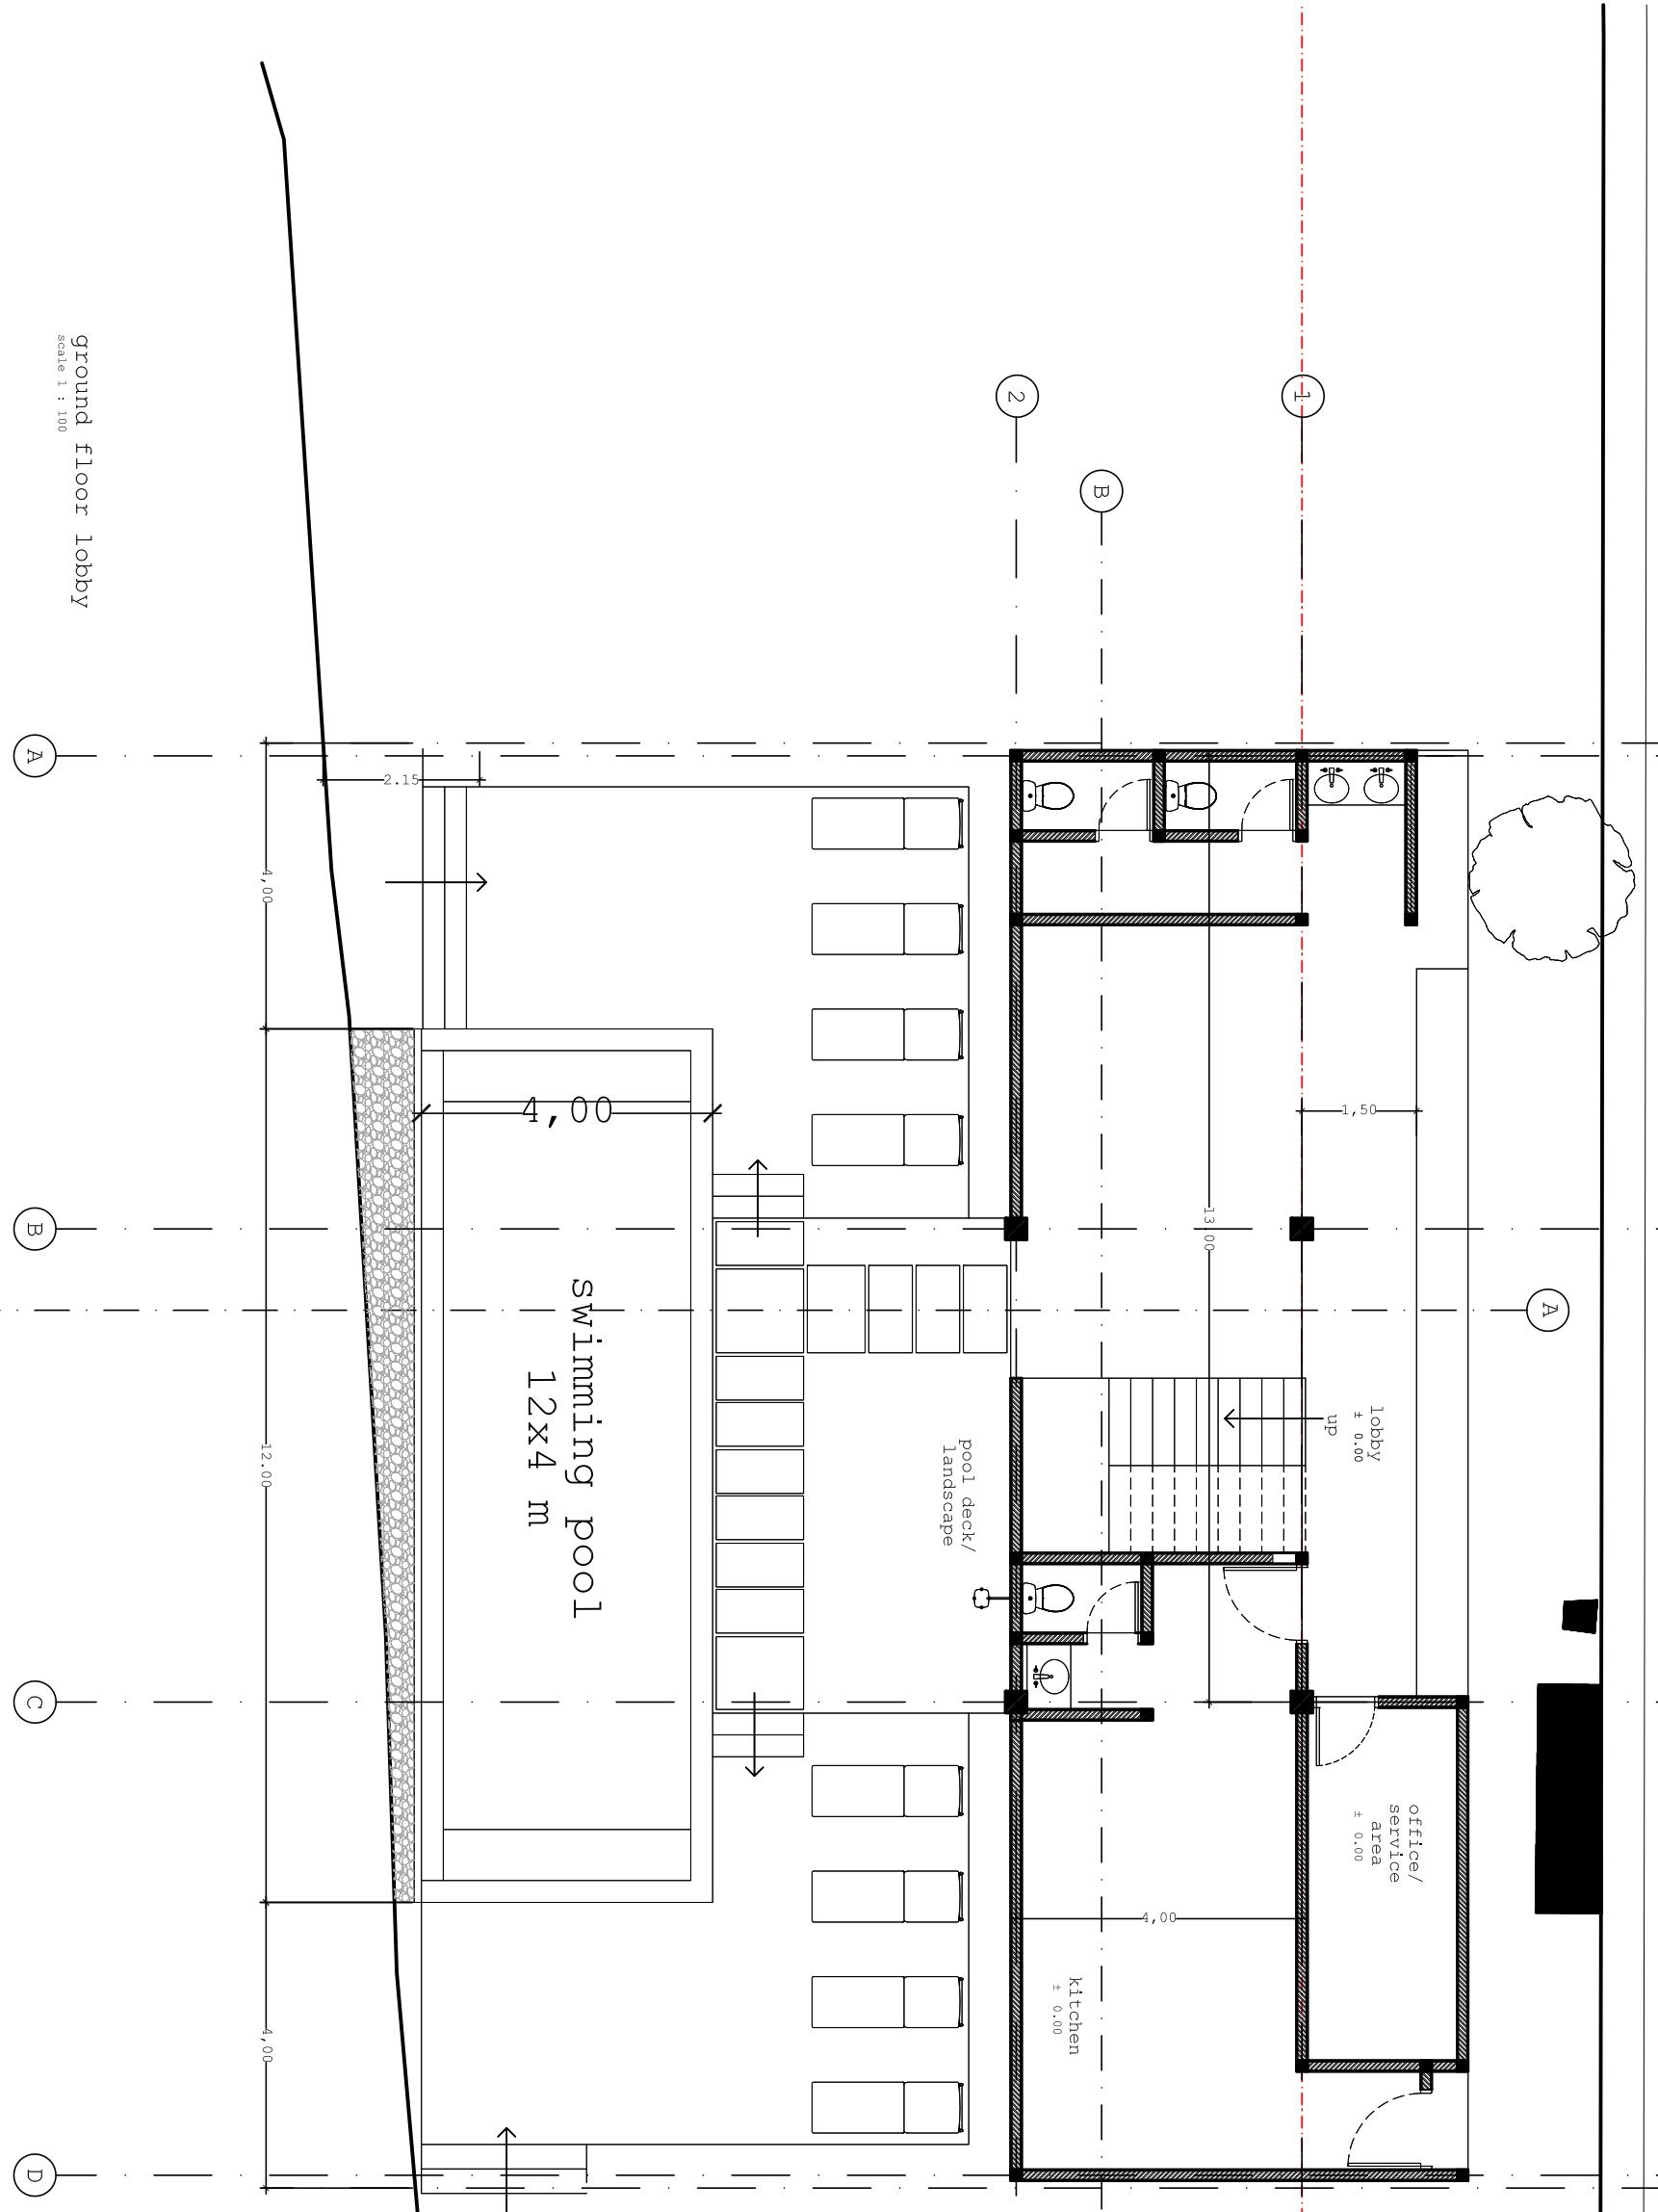

contractors must check all dimensions on site before starting any work or shop drawings.		<u>project title</u>	checked
		apartment	moka
<u>client</u>	mr . paul	<u>category</u>	development drawing
		<u>scale</u>	A3 - 1:100
		<u>revision</u>	
		<u>date</u>	25 january 2021
		<u>drawing number</u>	A-2.1

moka studio

design and build

second floor lobby
scale 1 : 100

(A)

(B)

(C)

(D)

6.50

6.50

1.58

dining area
+ 3.45

dining area
+ 3.45

(1)

(2)

(A)

corridor

down

corridor

contractors must check all dimensions on site before starting any work or shop drawings.
figured dimensions to take precedence over scale readings.

this drawing is copyright and property of the architects

project title
apartment

checked

category

moka

development drawing

scale

A3 - 1:100

client

approved

revision date
25 january 2021

drawing number
A-2.2

moka studio

design and build

section a

scale 1 : 75

note : all structure design need recommendation from structure engineering

contractors must check all dimensions on site before starting any work or shop drawings. figured dimensions to take precedence over scale readings.

this drawing is copyright and property of the architects

A

B

C

building section a

61.00

60.50

60.00

61.50

62.00

62.50

63.00

63.50

64.00

FFL ± 3.50

FFL ± 6.50

FFL ± 9.00

1.50

4.00

13.50

4.00

1.00

3.00

1.54

1.96

0.90

3.66

1.54

1.96

0.90

3.66

0.90

moka studio


design and build

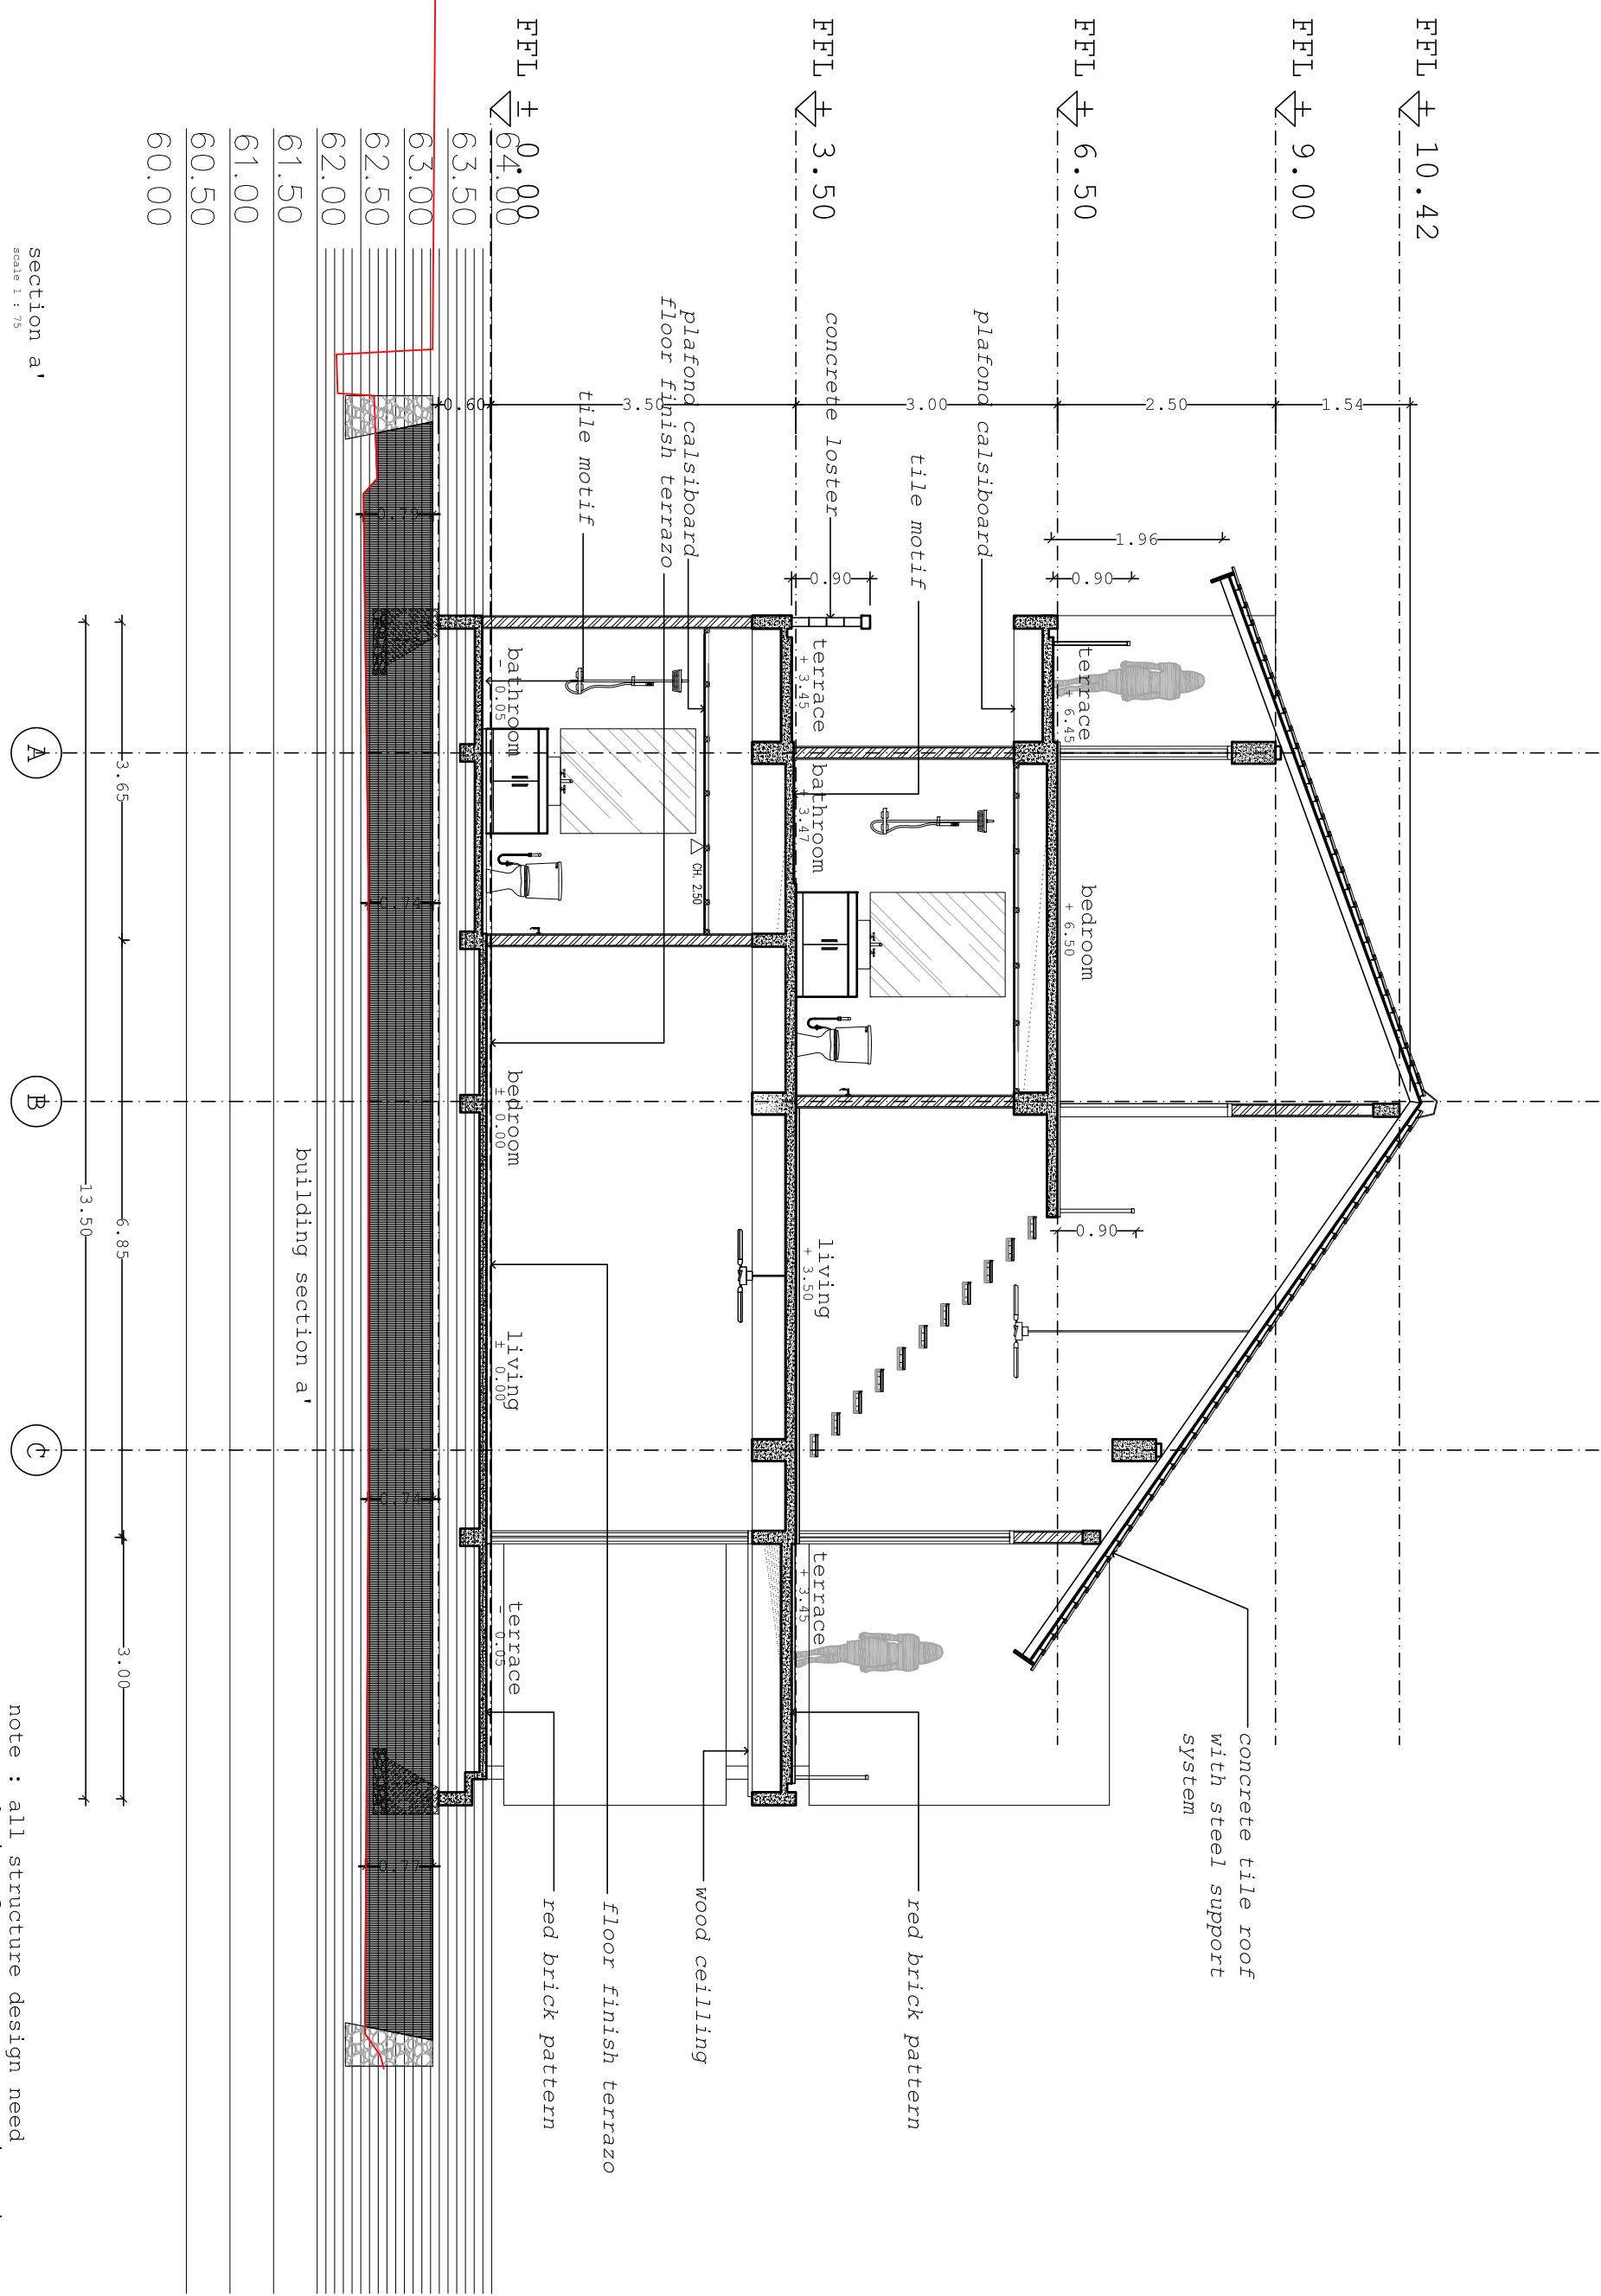

note : all structure design need recommendation from structure engineering

contractors must check all dimensions on site before starting any work or shop drawings.		<u>project title</u>	checked	<u>category</u>	development drawing	<u>scale</u>	A3 - 1:75	<u>drawing title</u>	building a building section	
figured dimensions to take precedence over scale readings.		<u>client</u>	moka	<u>approved</u>						
this drawing is copyright and property of the architects		mr. paul								

concrete tile roof
with steel support
system

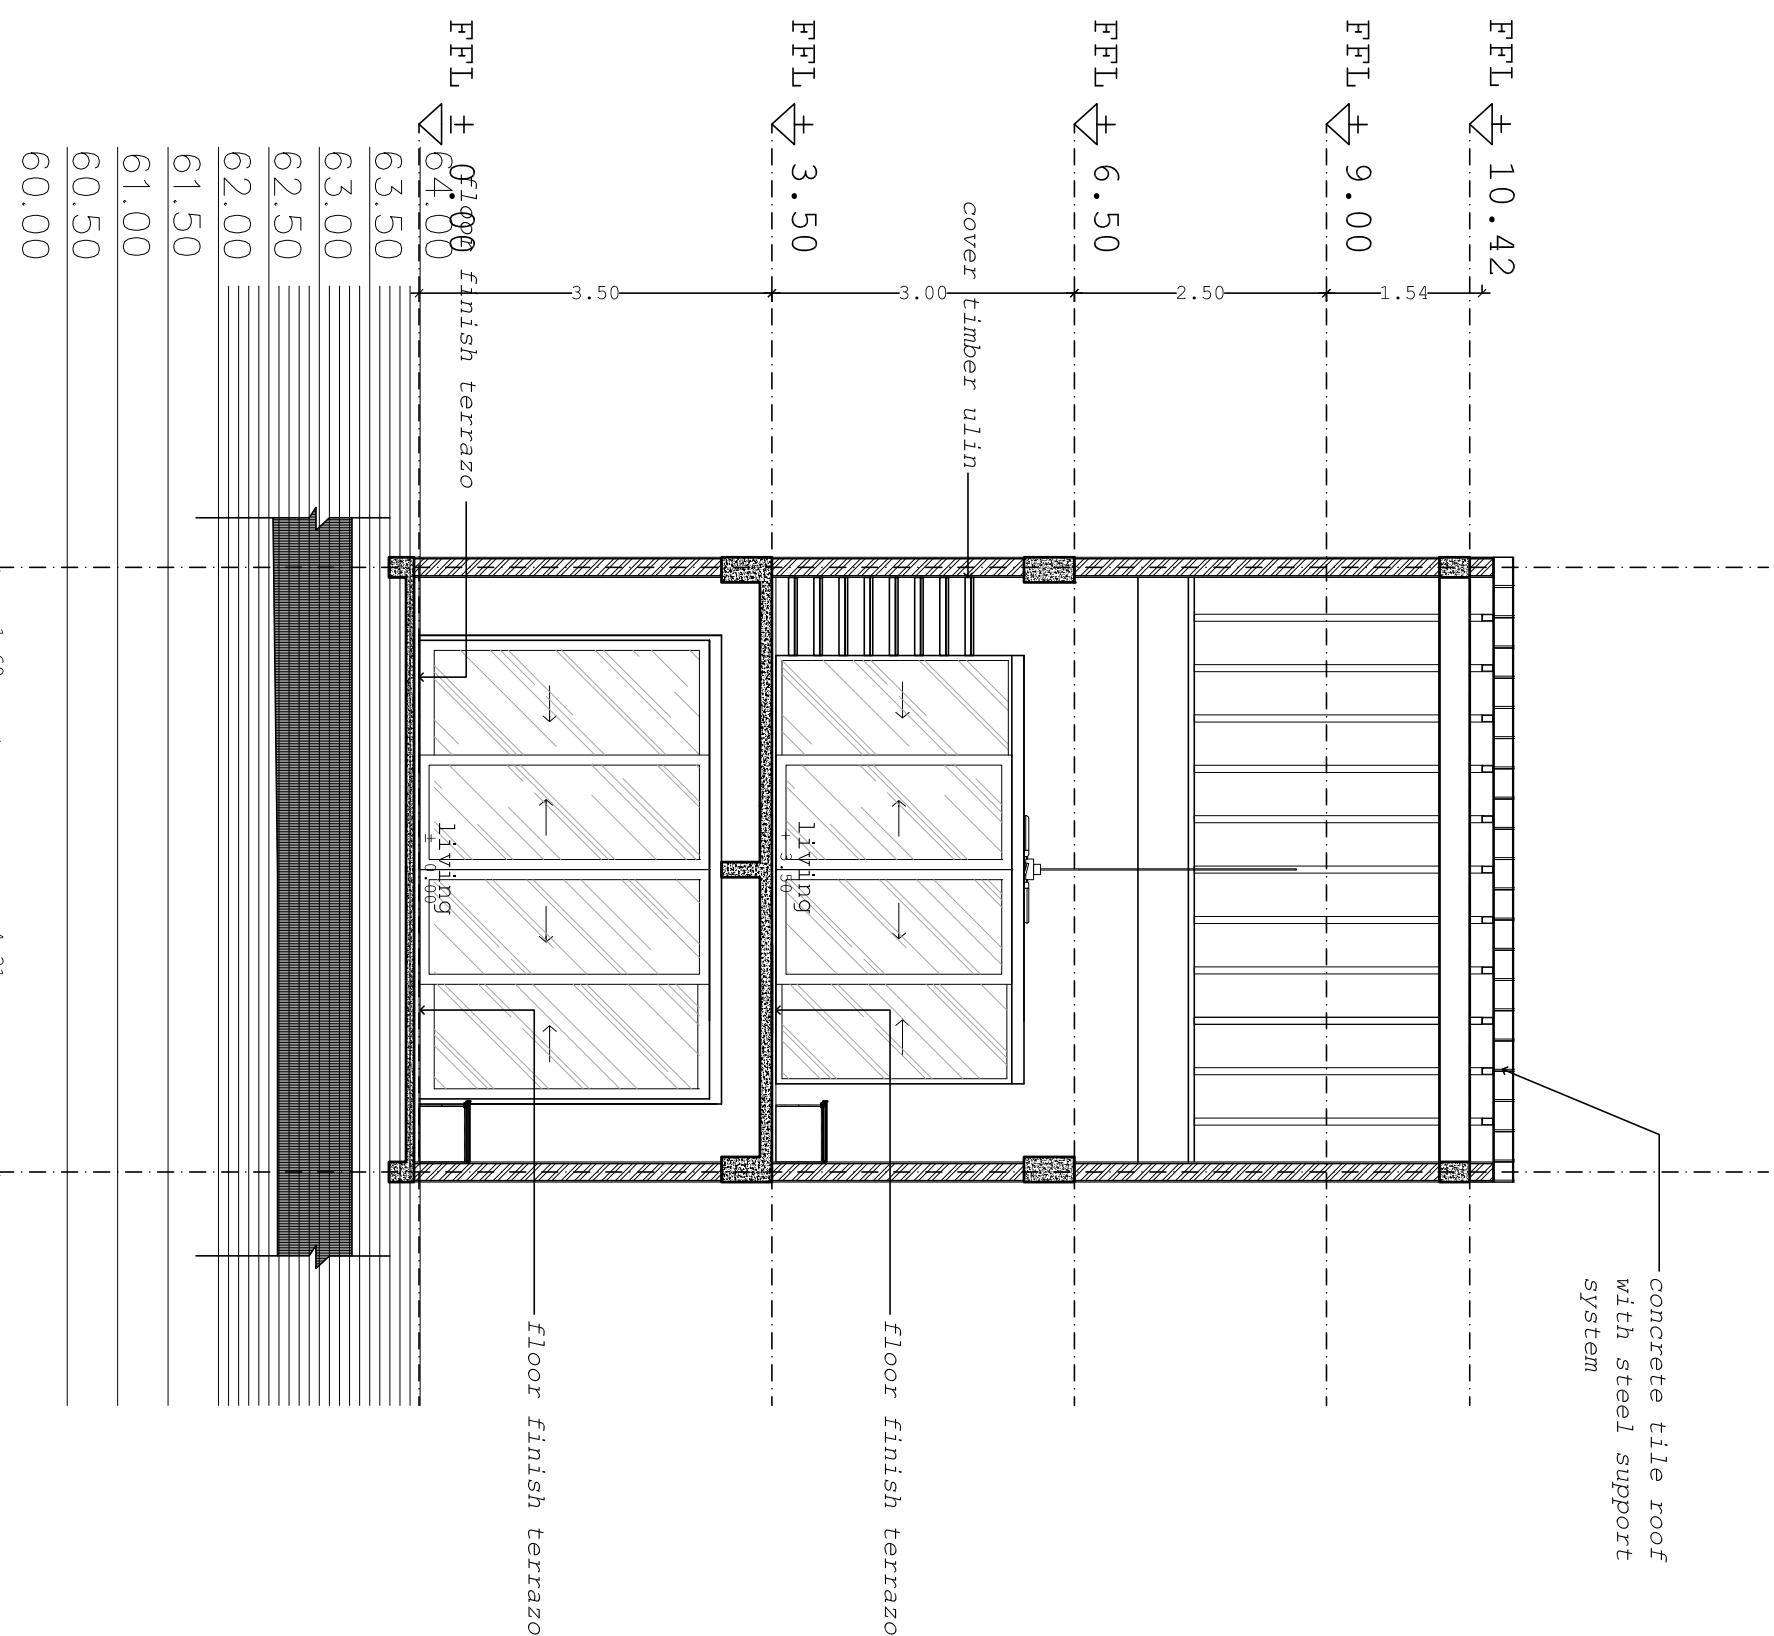

section b
scale 1 : 75

note : all structure design need
recommendation from structure engineering

project title	checked	category	scale	drawing title
apartment	moka	development drawing	A3 - 1:75	building a building section
client	mr. paul	revision	date	drawing number
			25 january 2021	A-4.3

moka studio
design and build


moka studio

design and build

Section C

figured dimensions to take precedence over scale readings.

note : all structure design need recommendation from structure engineering

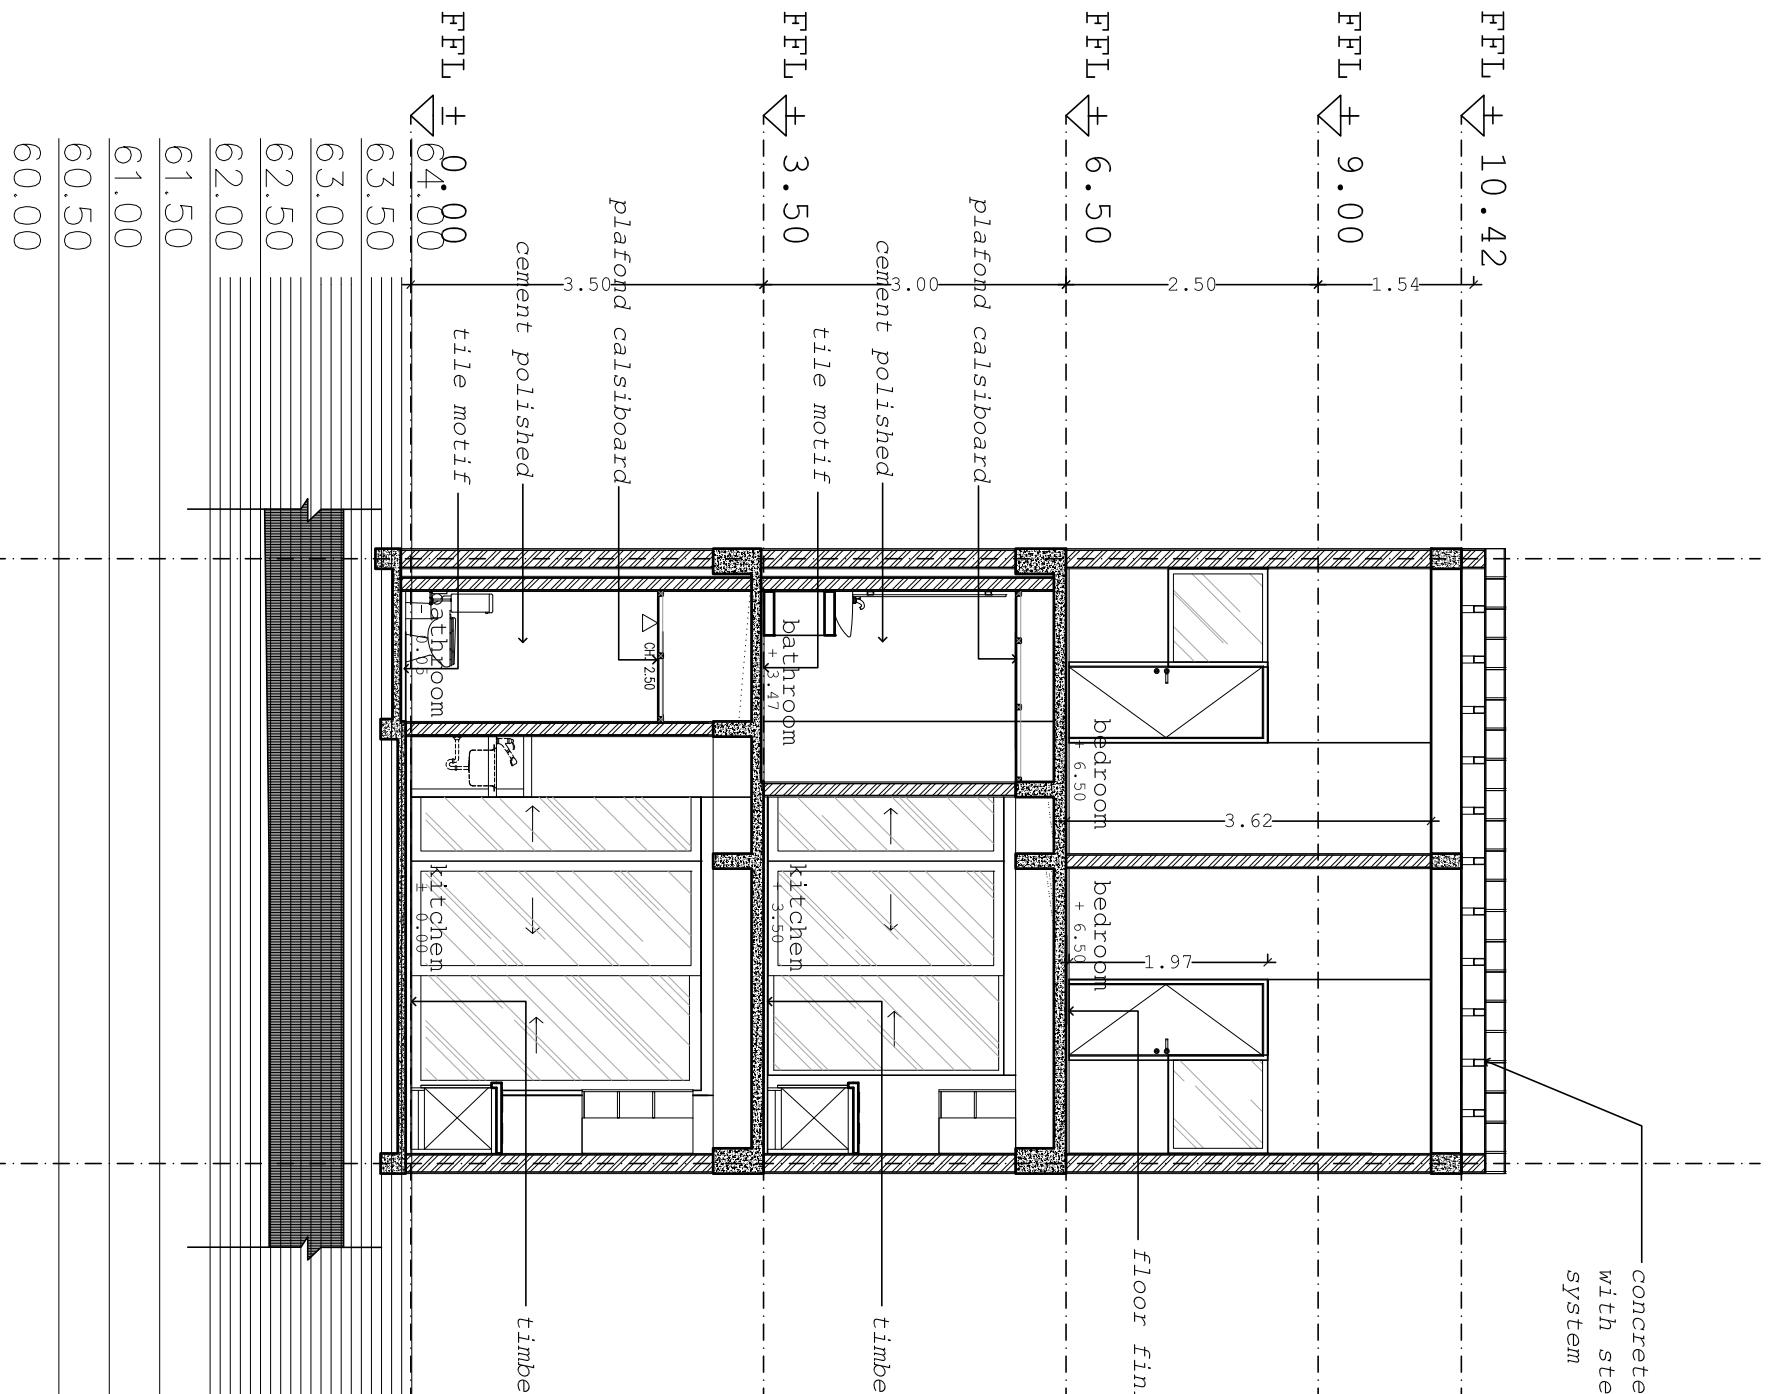

— concrete tile roof
with steel support system

<p>contractors must check all dimensions on site before starting any work or shop drawings.</p> <p>figured dimensions to take precedence over scale readings.</p> <p>this drawing is copyright and property of the architects</p>		<u>project title</u>	<u>checked</u>	<u>category</u>	<u>scale</u>	<u>drawing title</u>
<u>client</u>	apartment	moka	development drawing	A3 - 1:75	building a building section	
<u>approved</u>						
<u>revision</u>						
<u>date</u>	25 january 2021					
<u>drawing number</u>	A-4.4					

moka studio
design and build

design and build

Section a


A

3

Q

note : all structure design need recommendation from structure engineering

contractors must check all dimensions on site before starting any work or shop drawings.	
figured dimensions to take precedence over scale readings.	apartment
this drawing is copyright and property of the architects	moka
	development drawing
	A3 - 1:75
	building b
	building section
<u>project title</u>	<u>category</u>
<u>client</u>	<u>scale</u>
mr . paul	<u>drawing title</u>
	<u>revision</u>
	<u>date</u>
25	january 2021
	<u>drawing number</u>
	A-4.1

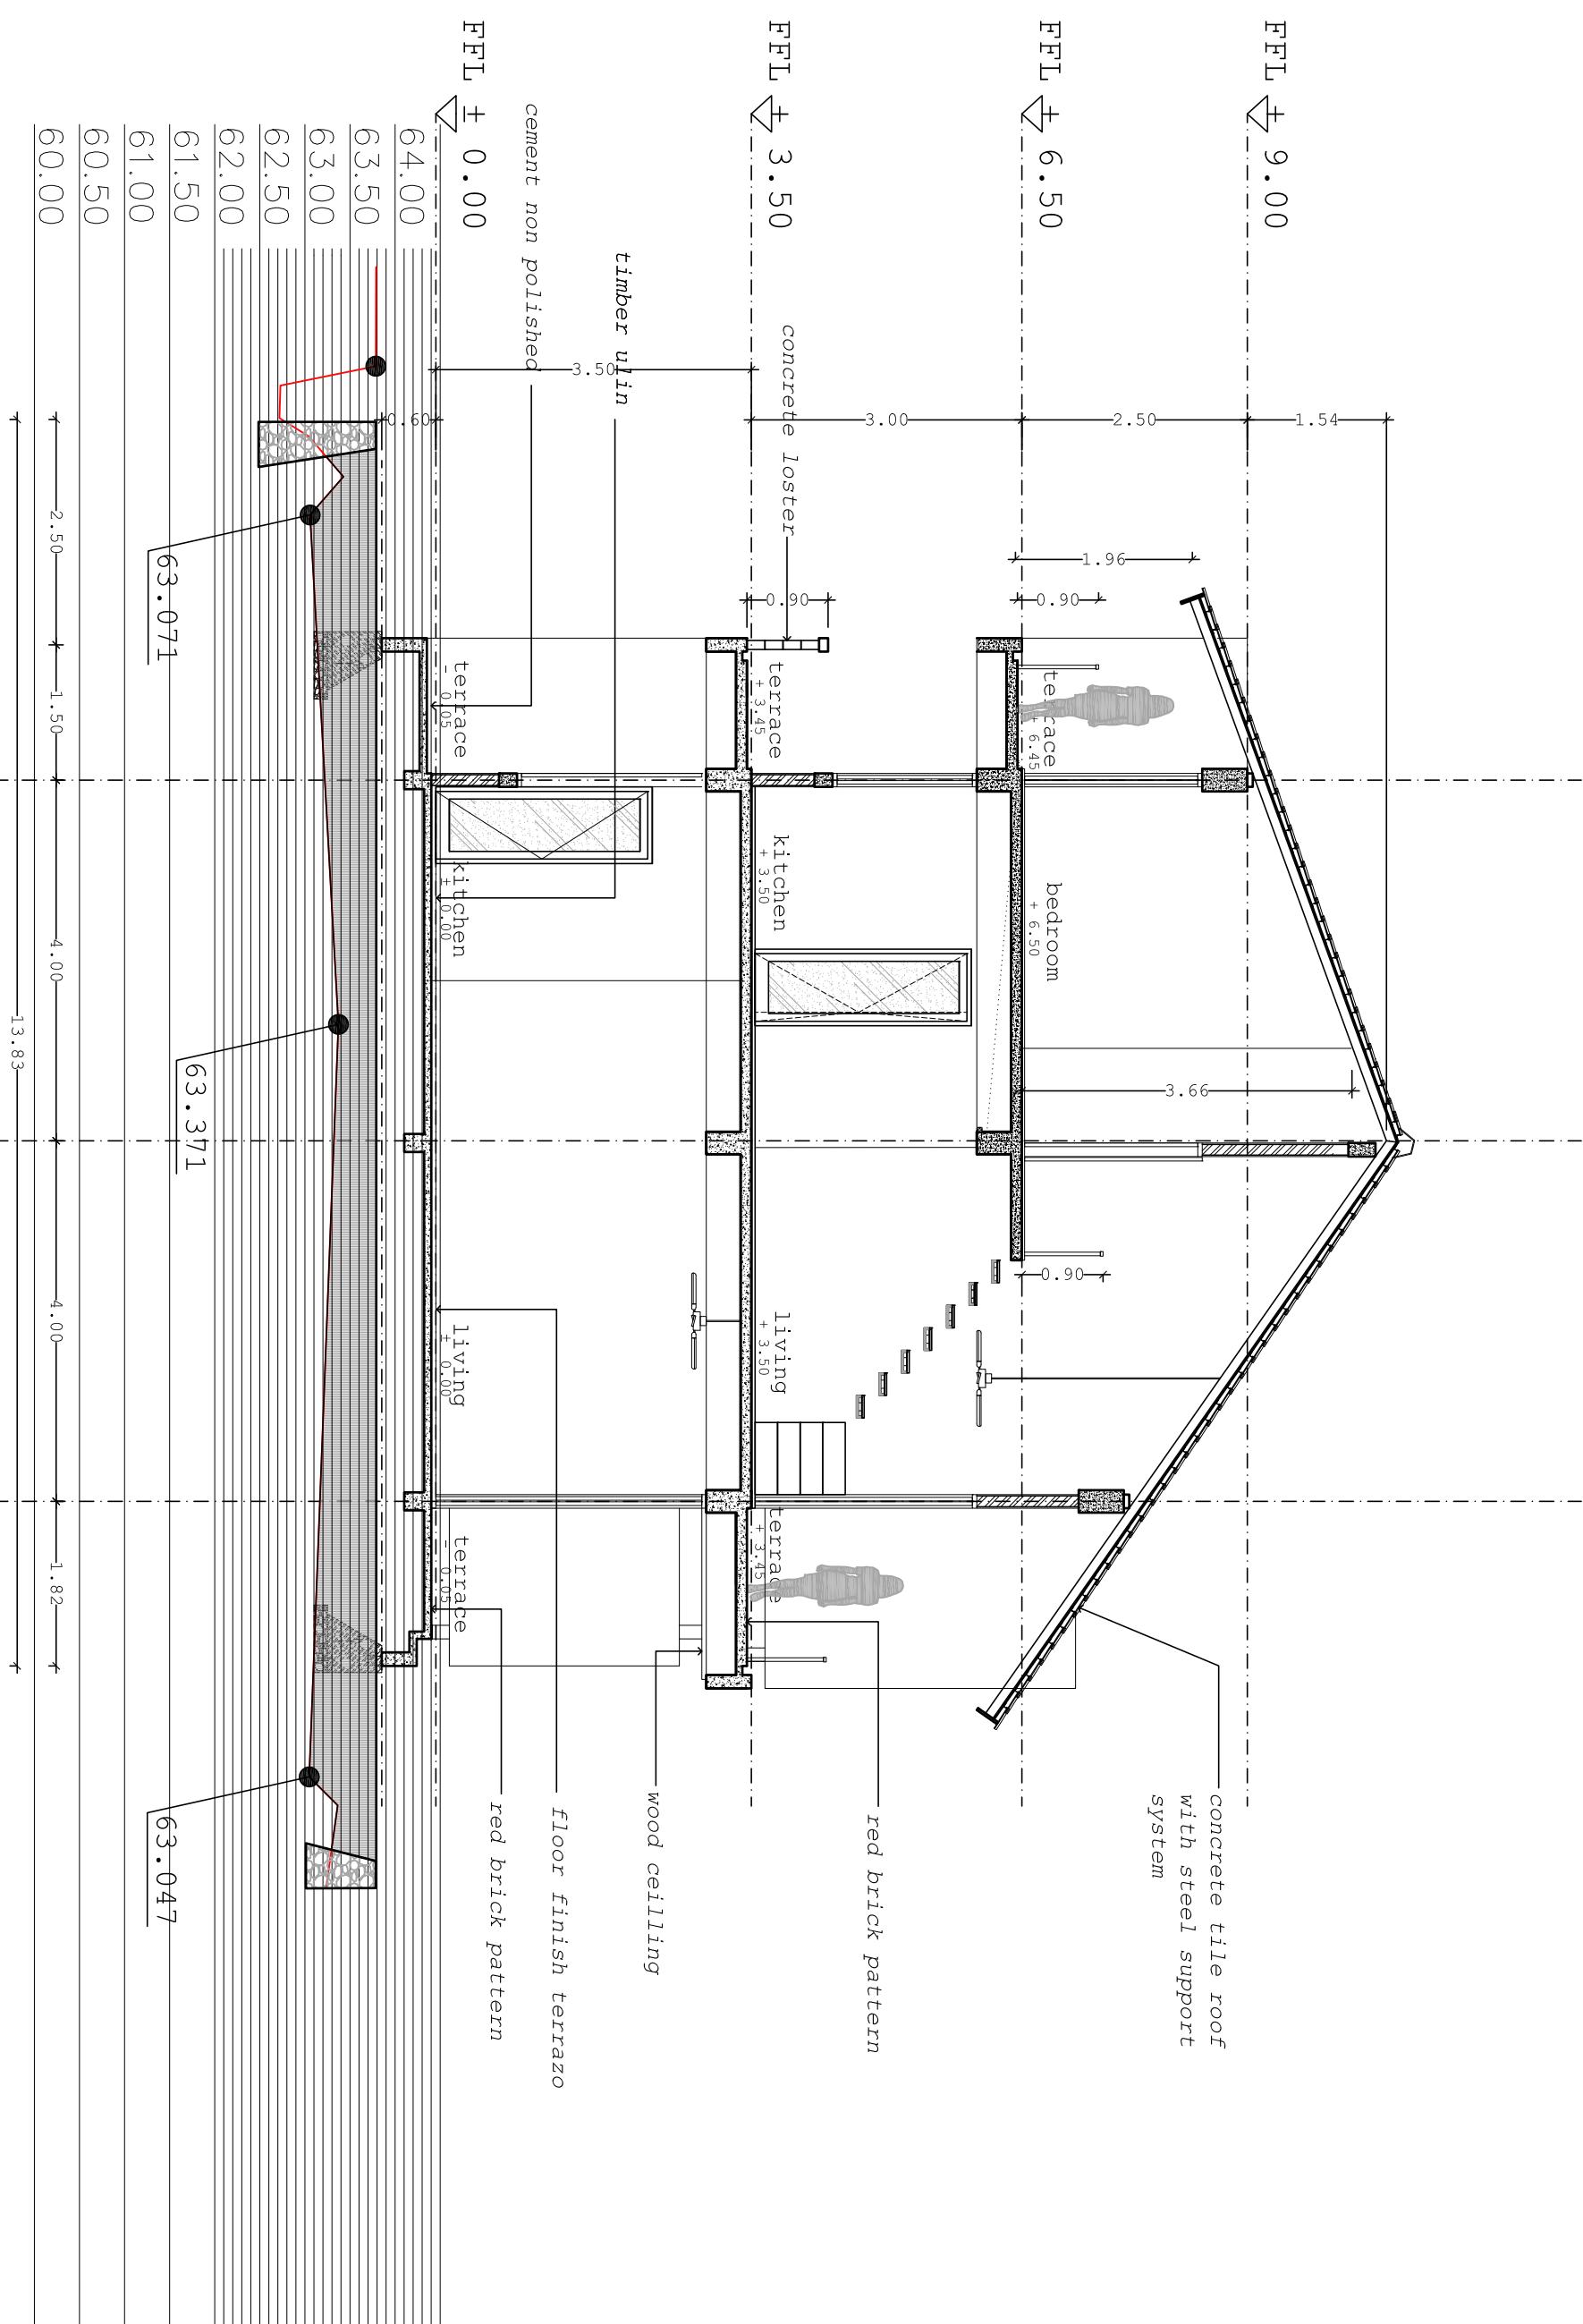

moka studio
design and build


design and build

Section a
scale 1 : 75


figured dimensions to take precedence over scale readings.

This drawing is copyright and property of the architects

note : all structure design need recommendation from structure engineering

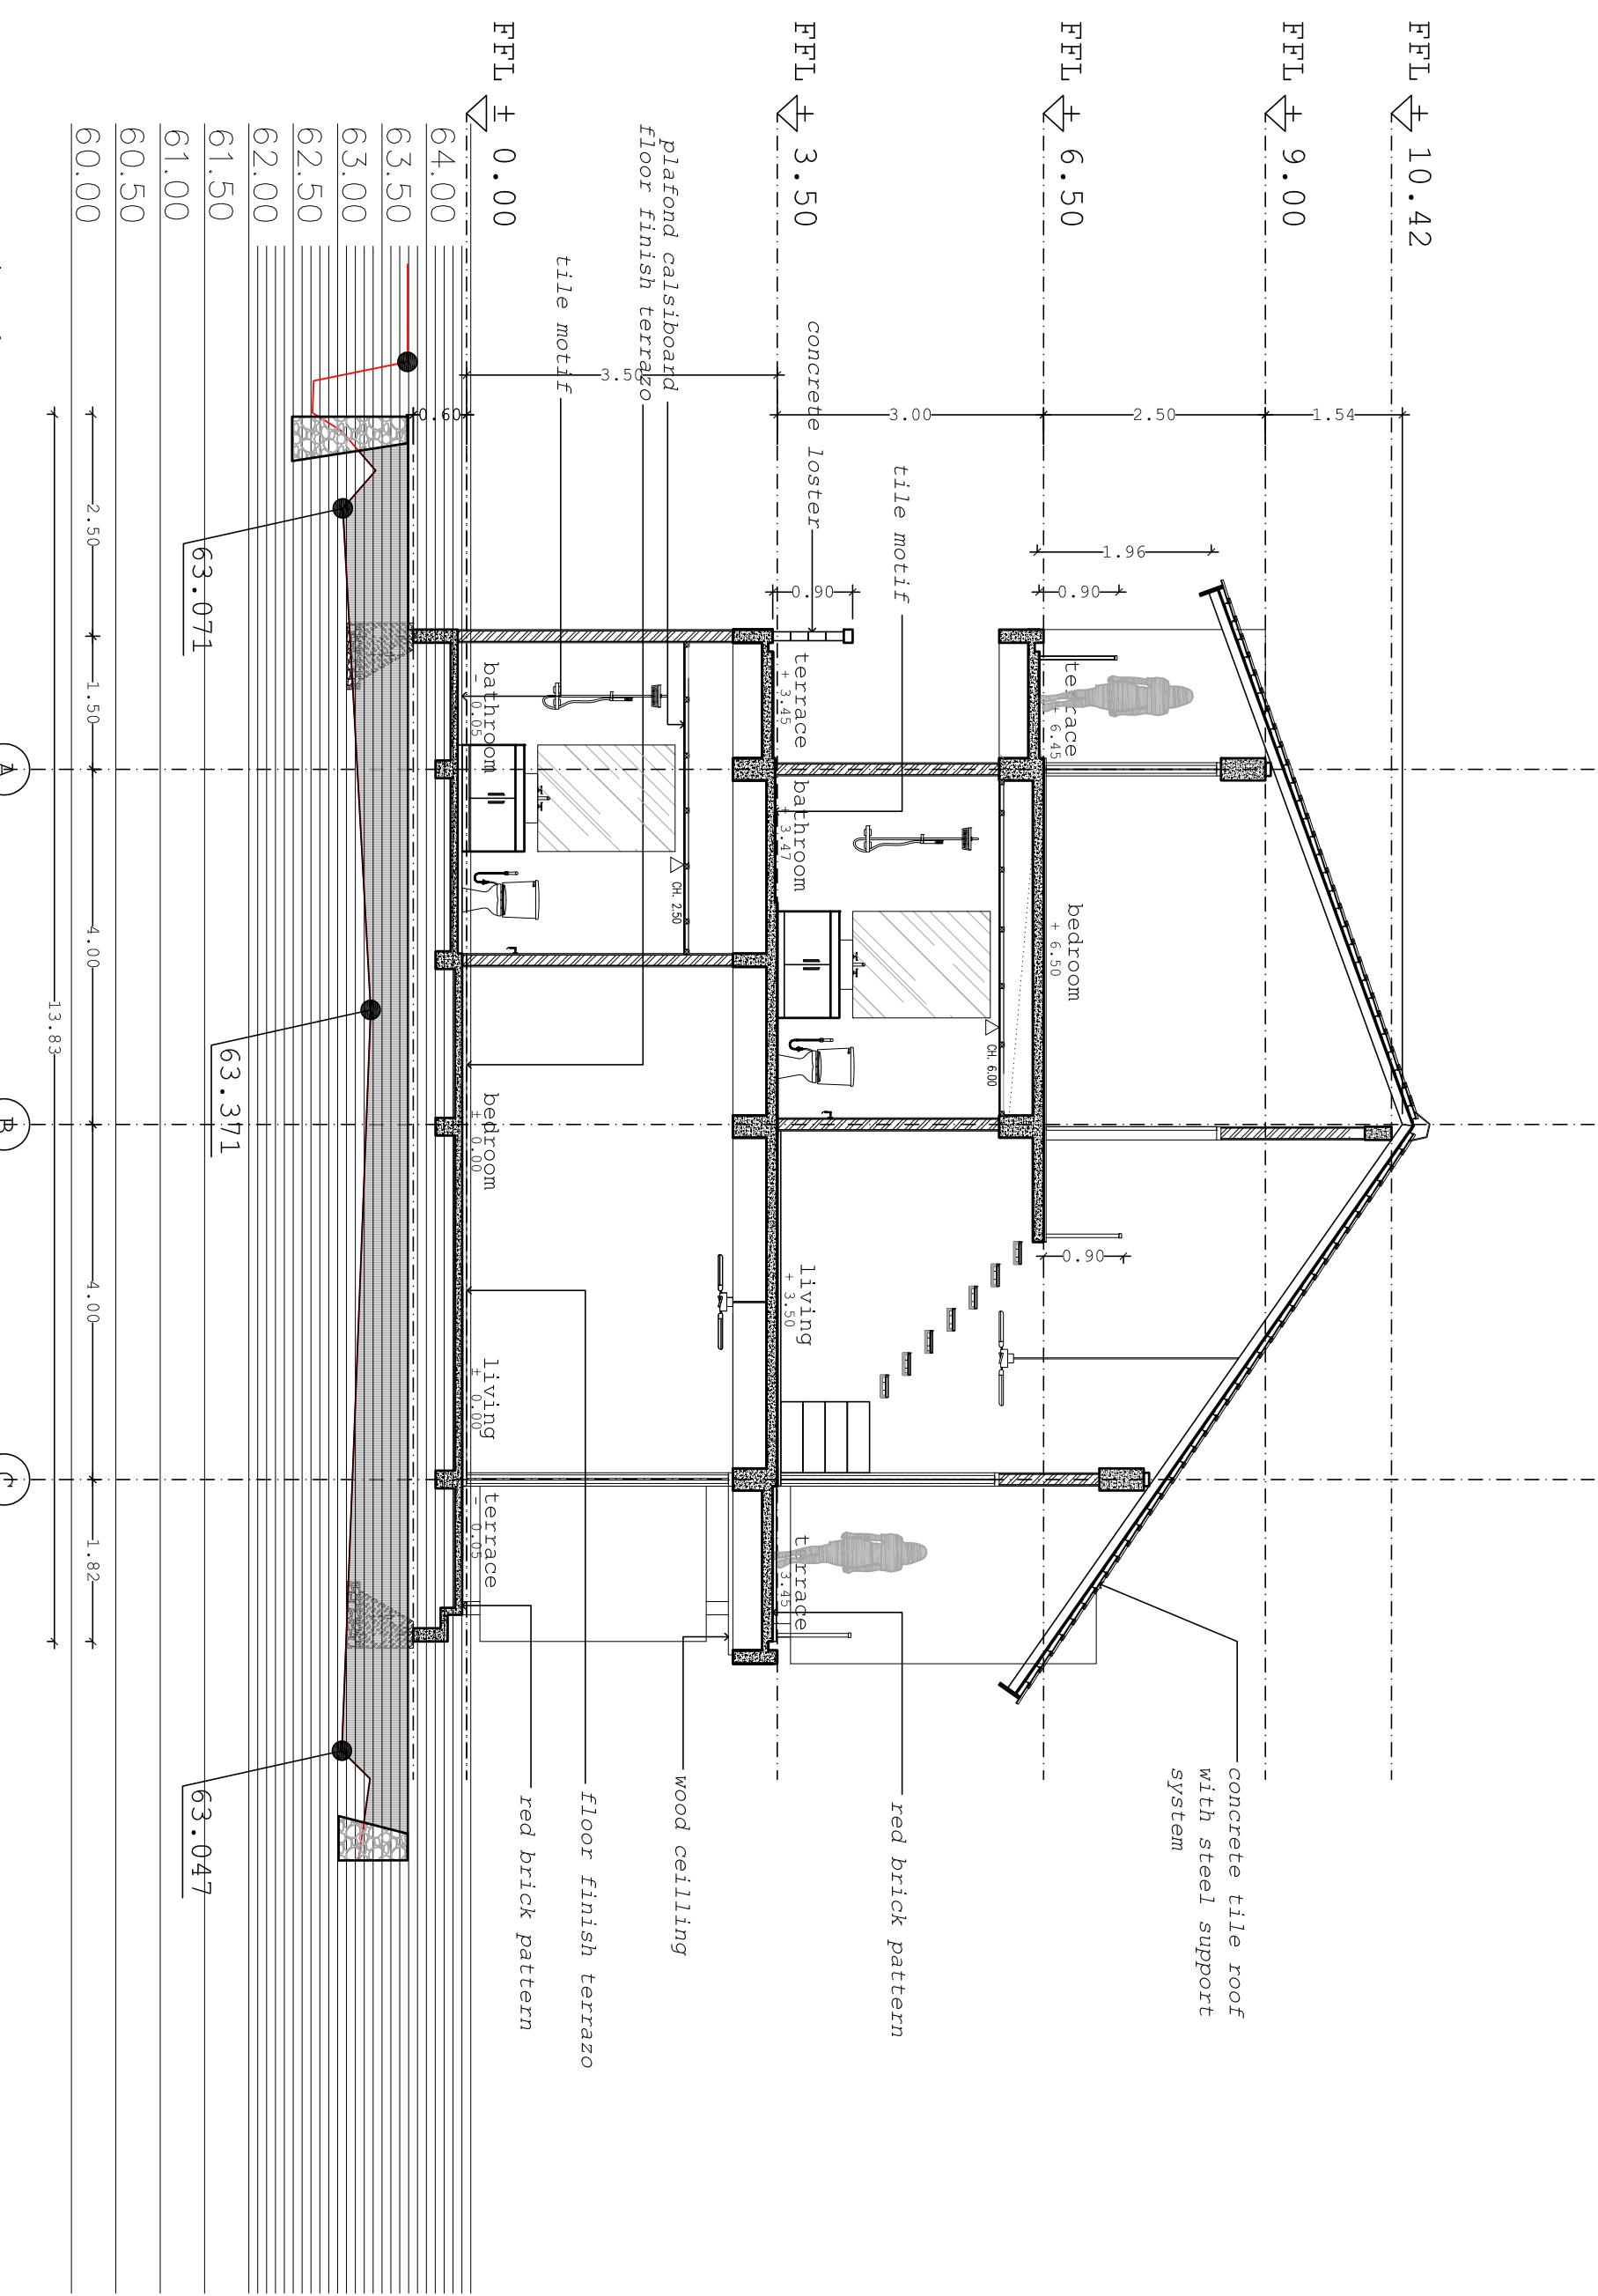

concrete tile roof
with steel support
system

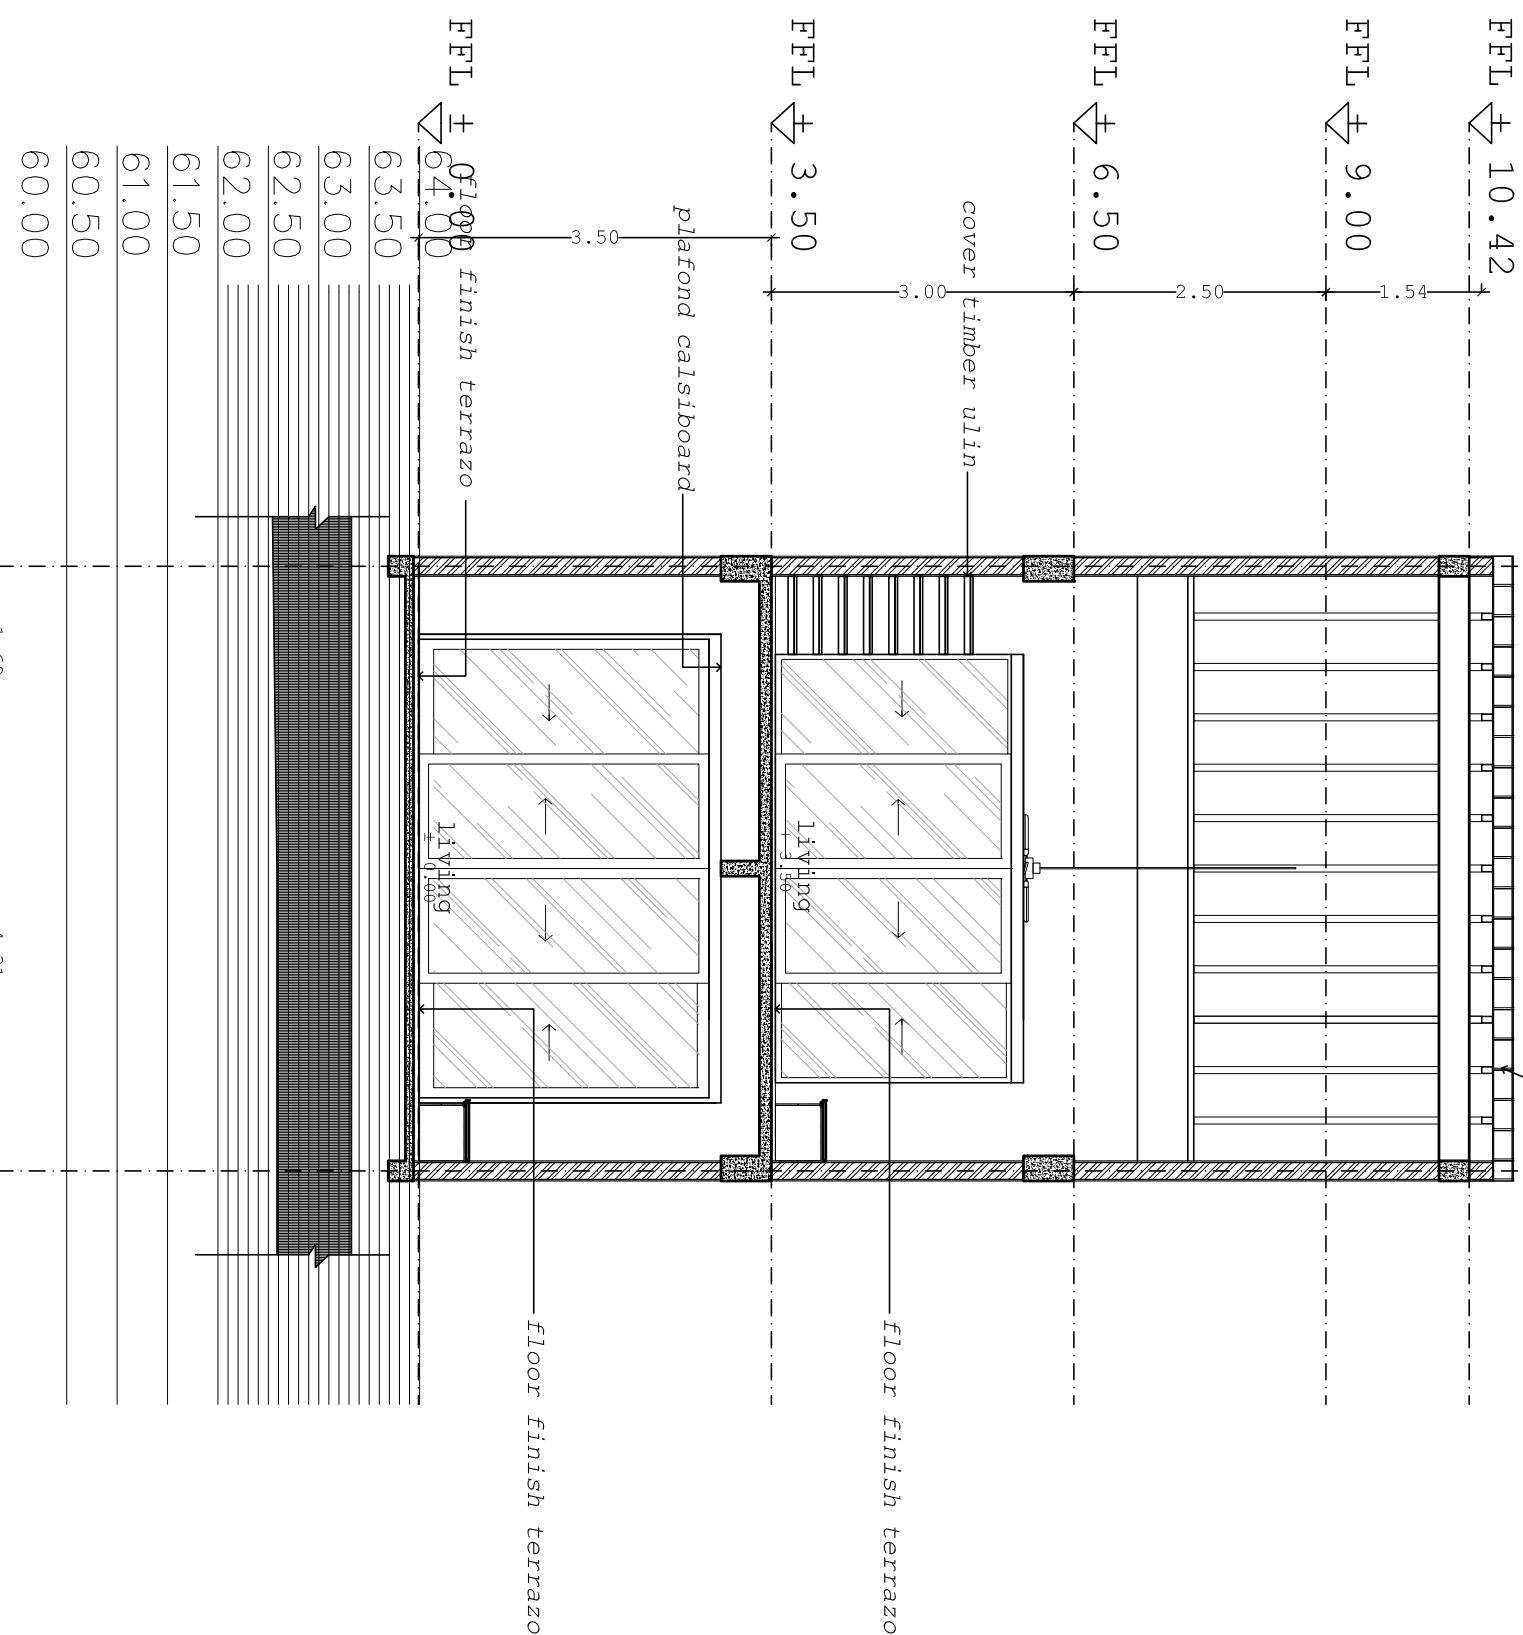


section b
scale 1 : 75

note : all structure design need
recommendation from structure engineering

project title	checked	category	scale
apartment	moka	development drawing	A3 - 1:75
client		revision	date
mr. paul		25	january 2021
contractors must check all dimensions on site before starting any work or shop drawings.	figured dimensions to take precedence over scale readings.	drawing number	A-4.3
this drawing is copyright and property of the architects			

moka studio
design and build

concrete tile roof
with steel support
system

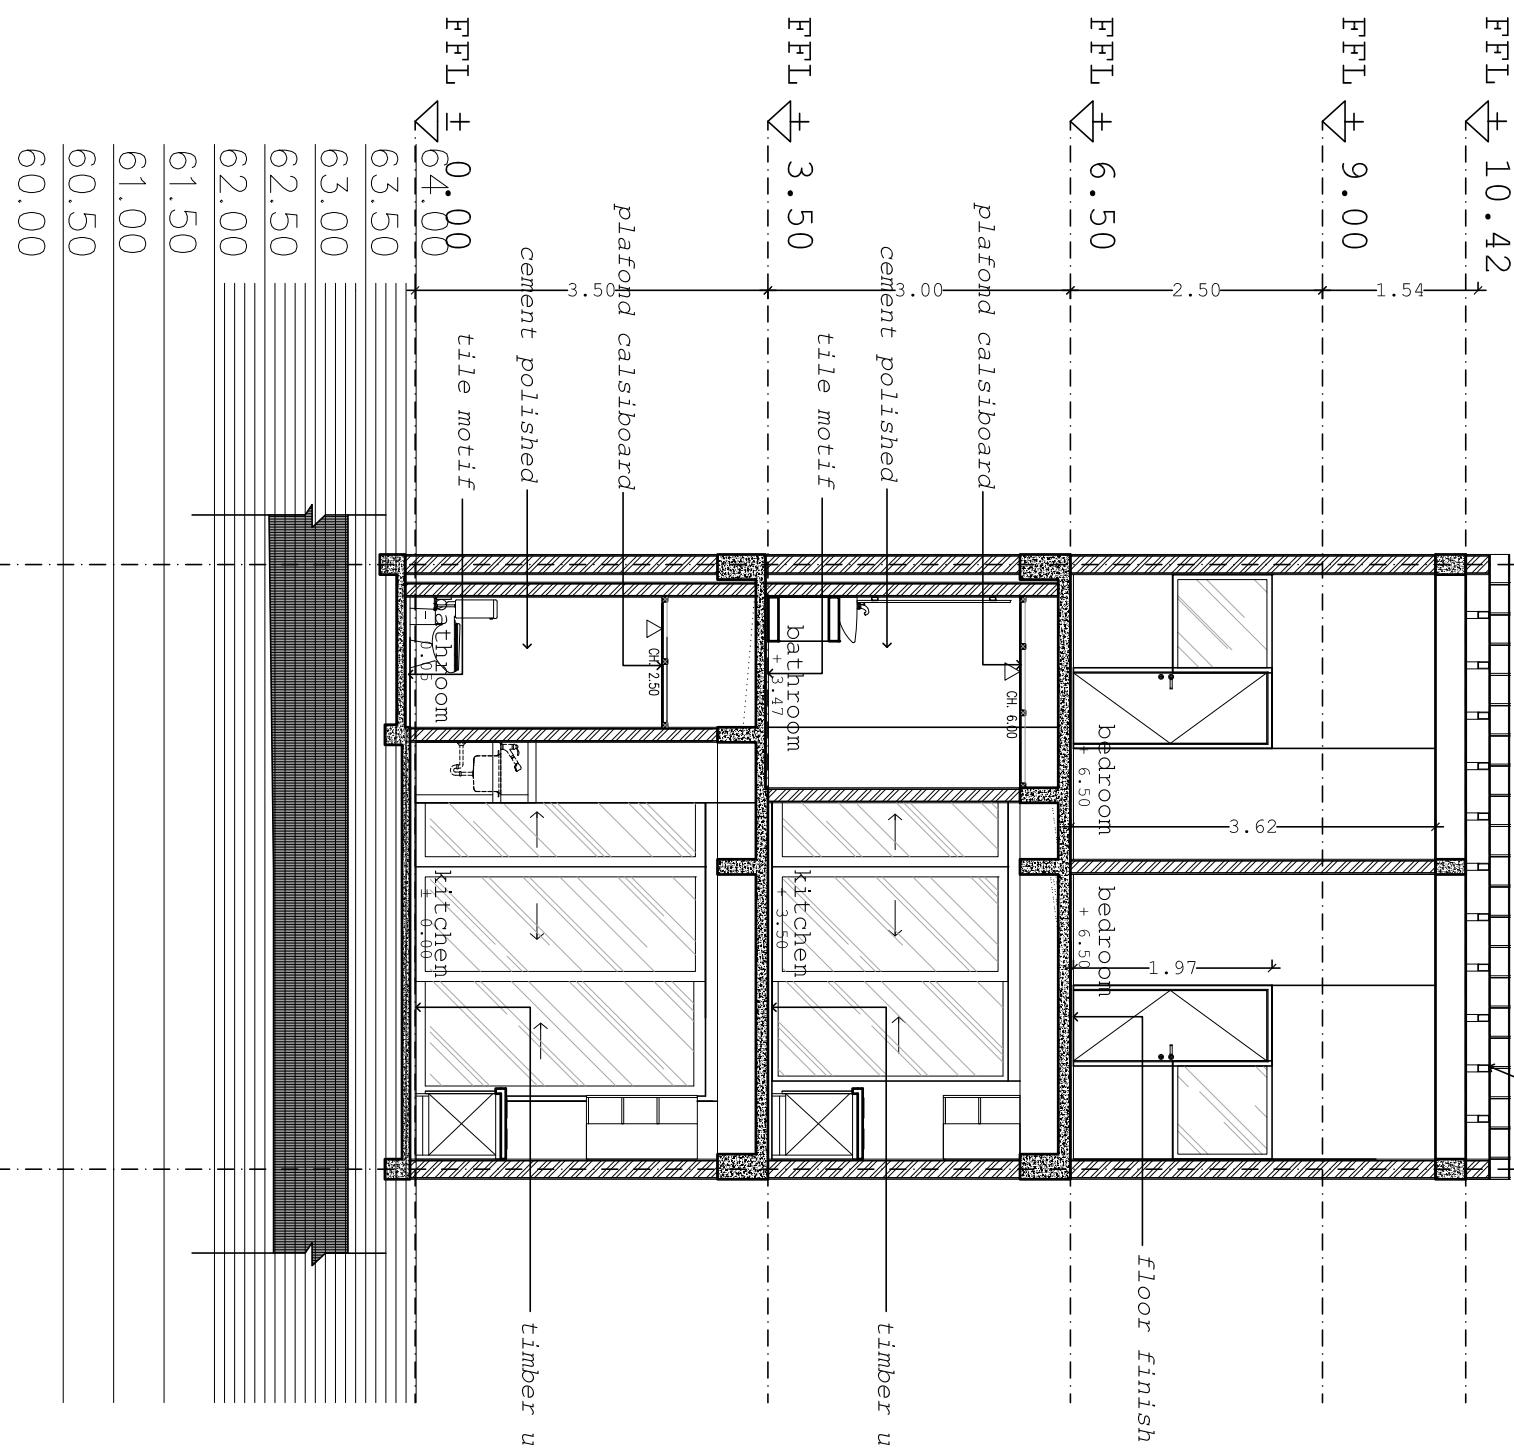

section c
scale 1 : 75

note : all structure design need
recommendation from structure engineering

contractors must check all
dimensions on site before
starting any work or shop
drawings.

figured dimensions to take
precedence over scale
readings.

moka studio
design and build

this drawing is copyright and
property of the architects

project title
apartment

checked
moka

category
development drawing

scale
A3 - 1:75

drawing title
building b
building section

client
mr. paul

approved

revision


date
25 january 2021

number
A-4.4

moka studio

design and build

section A
scale 1 : 100

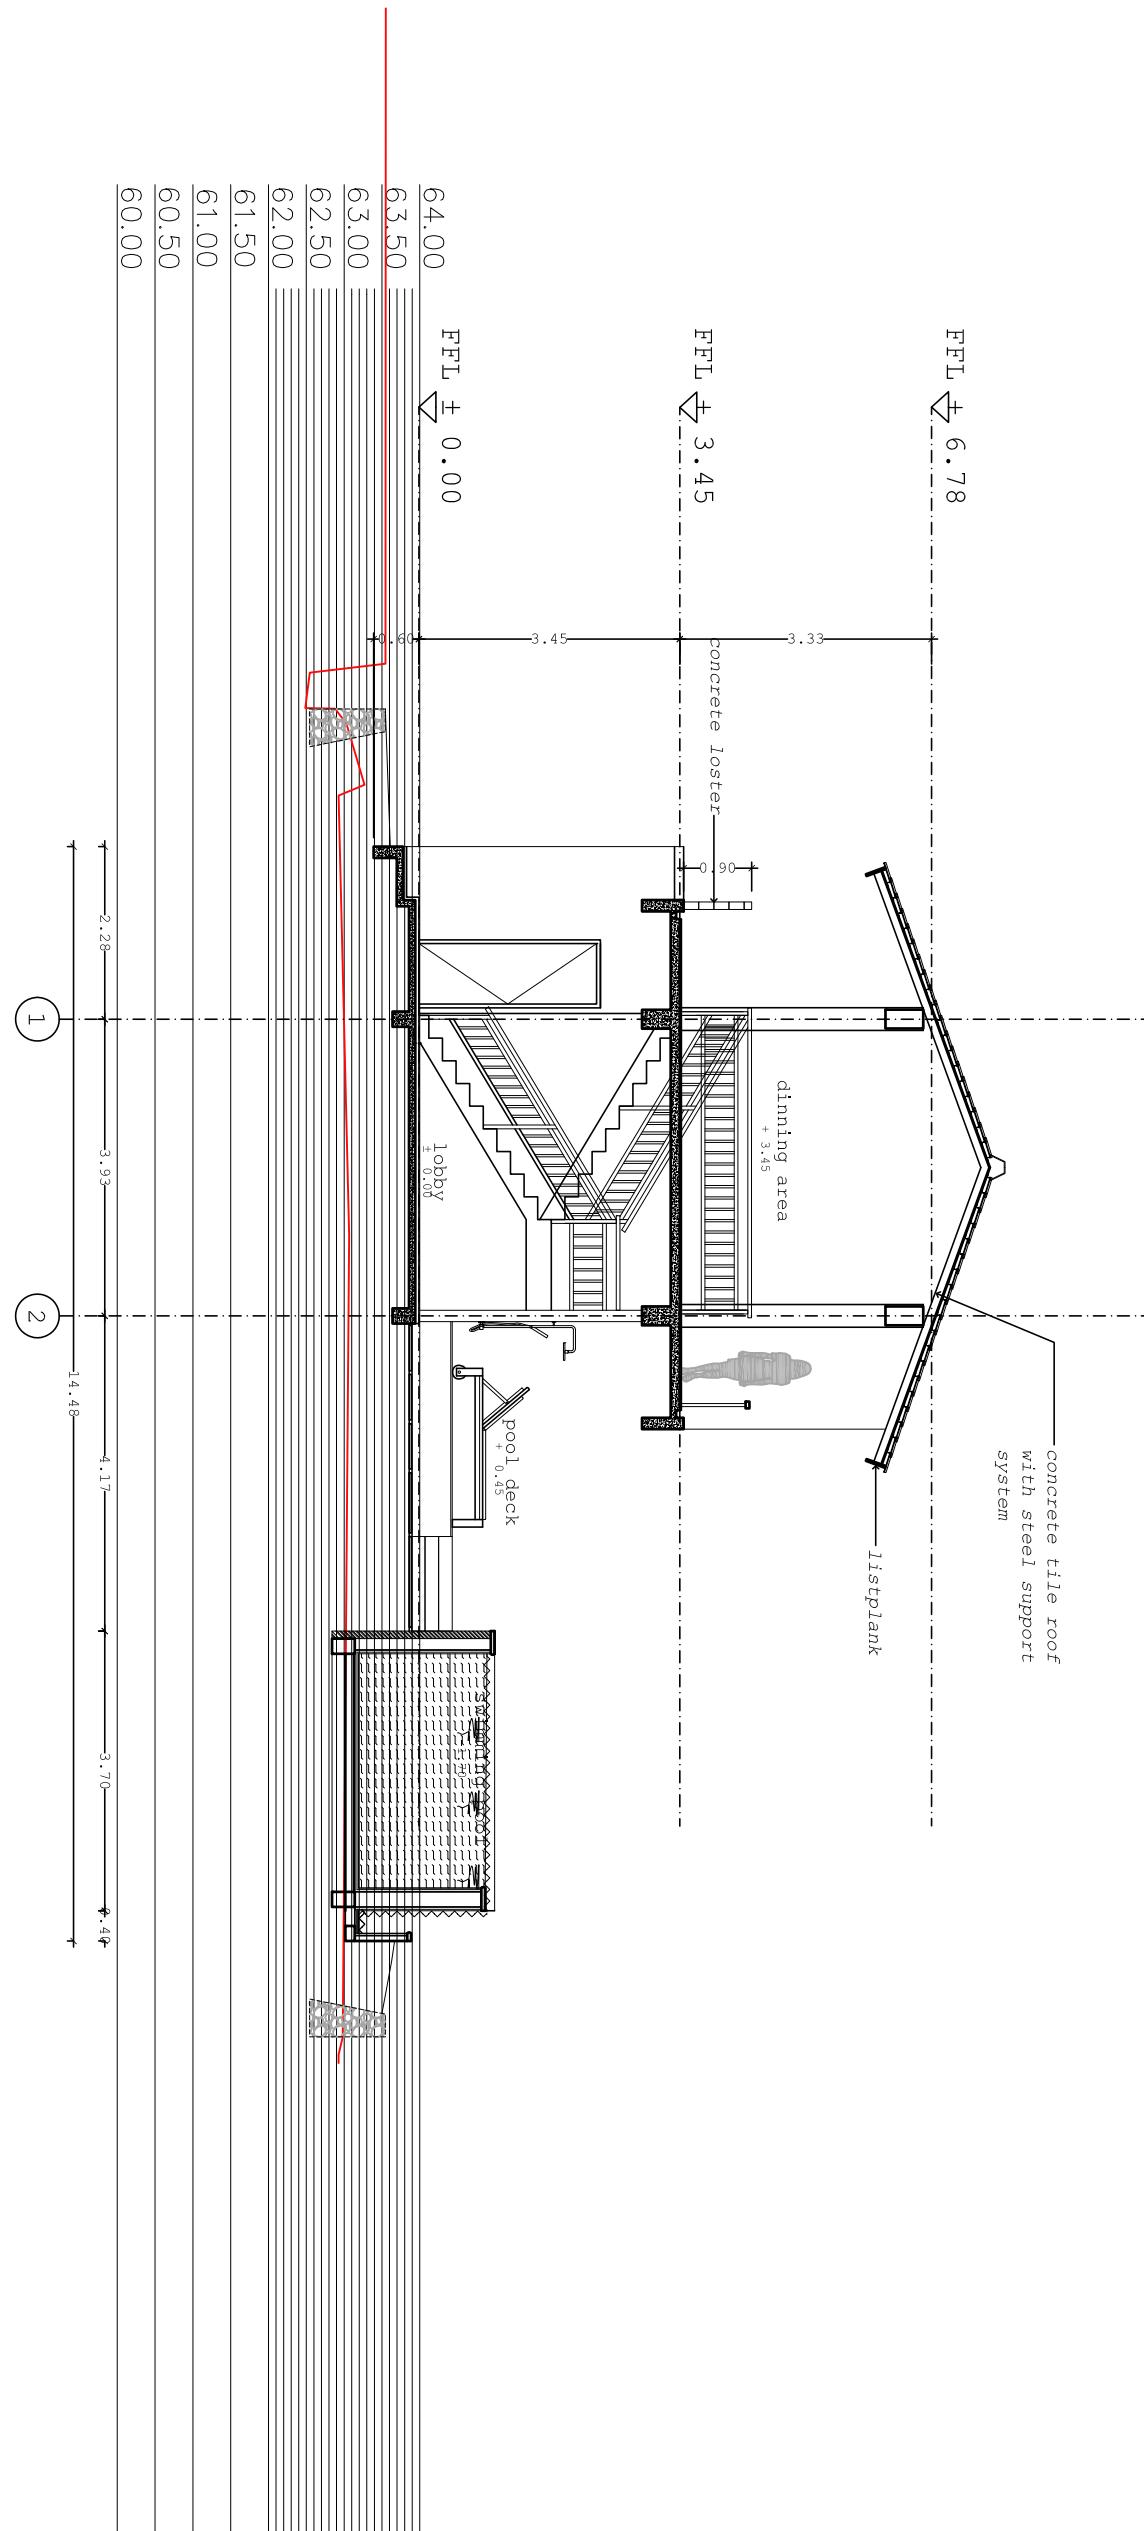

contractors must check all dimensions on site before starting any work or shop drawings. figured dimensions to take precedence over scale readings.

this drawing is copyright and property of the architects

project title	checked	category	scale
apartment	moka	development drawing	A3 - 1:100
client	approved	revision	date
mr. paul		25	january 2021


drawing title
lobby building section

drawing number
A-4.1

moka studio

design and build

section B
scale 1 : 100

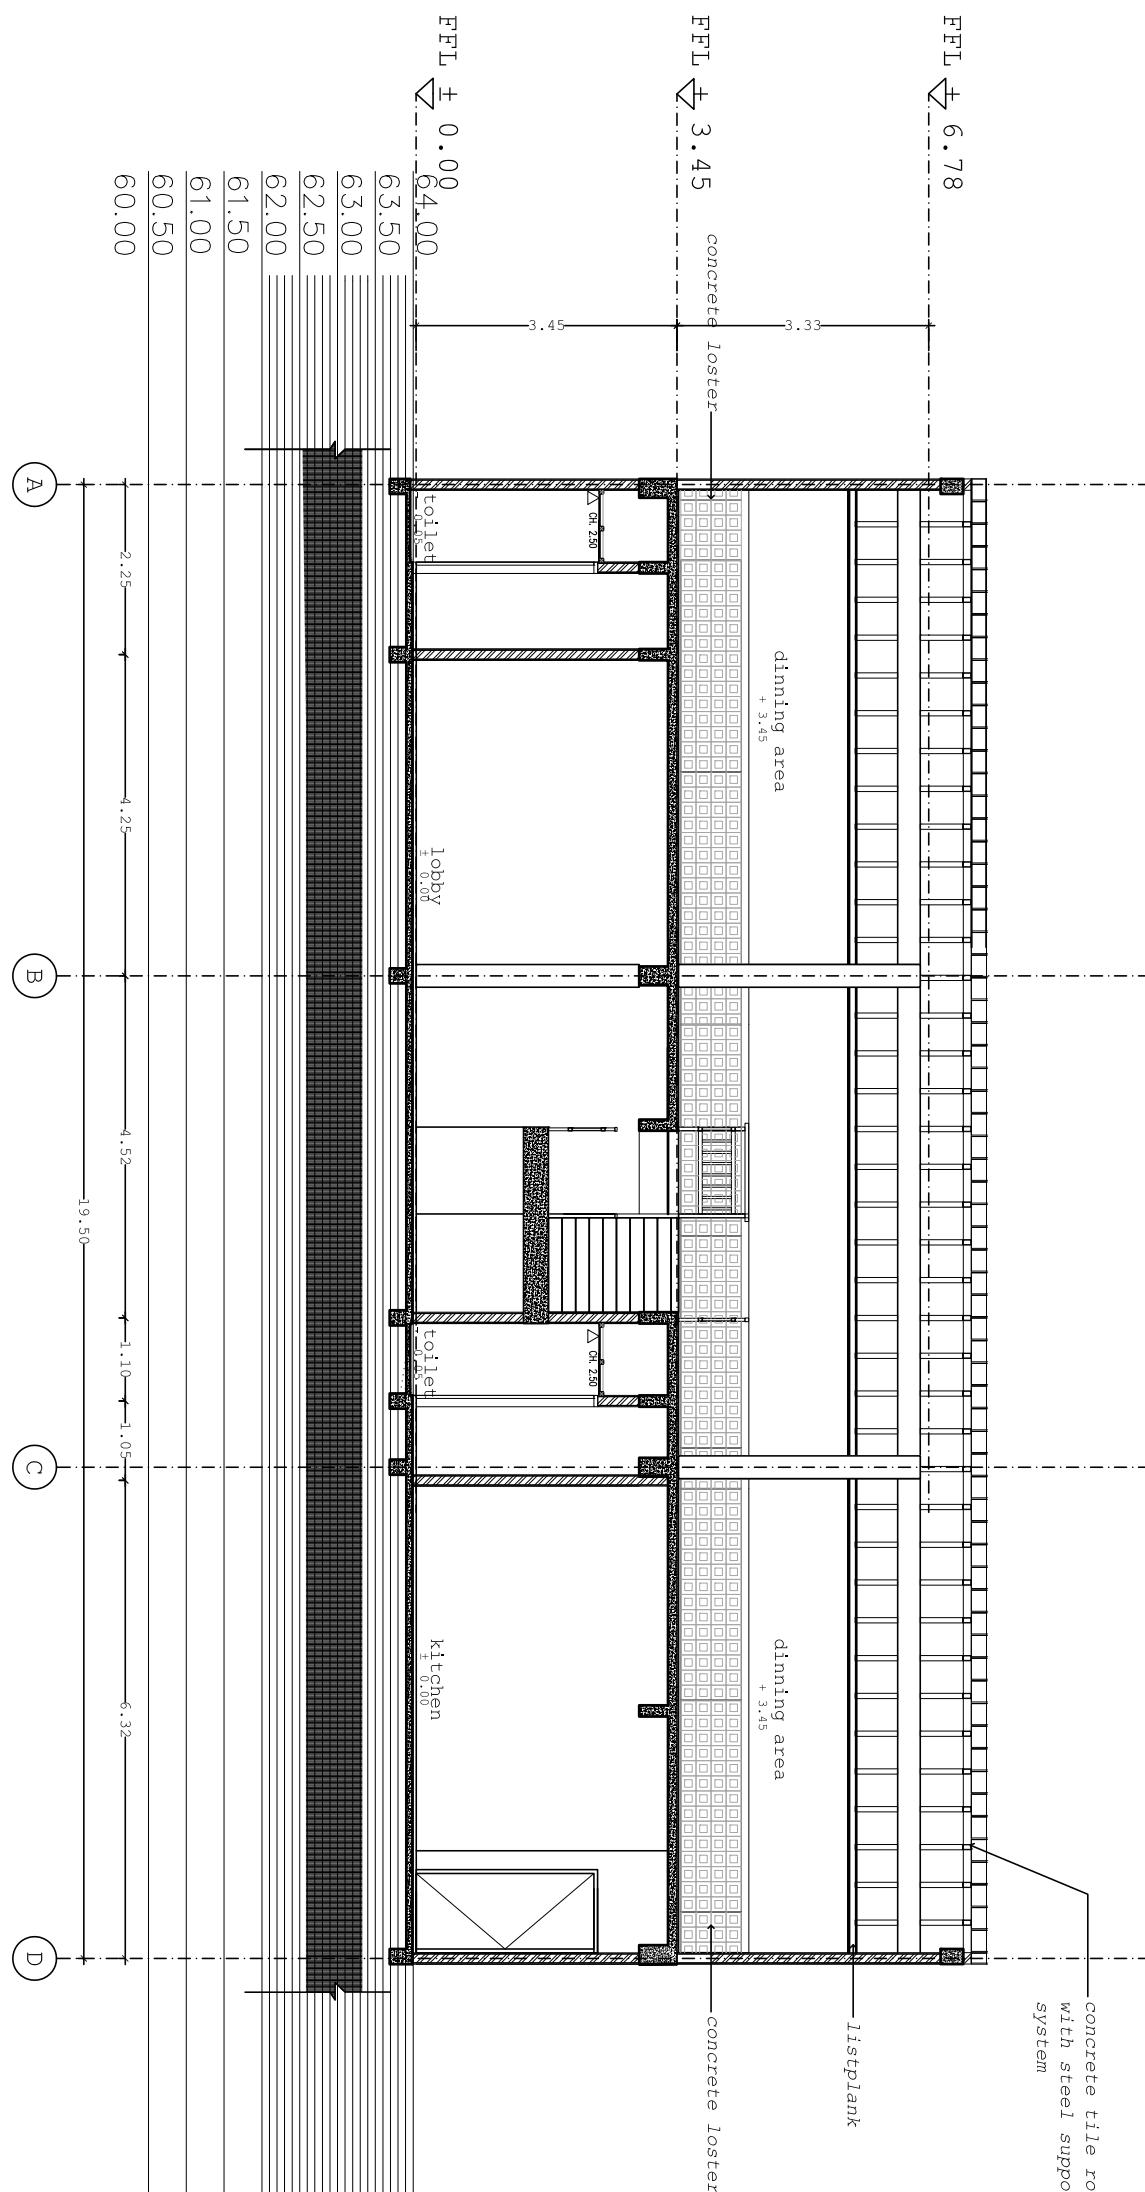

contractors must check all dimensions on site before starting any work or shop drawings. figured dimensions to take precedence over scale readings.

this drawing is copyright and property of the architects

project title	checked	category	development drawing	scale	A3 - 1:100
client	moka	title	lobby	number	
approved		revision	building section	date	25 january 2021

drawing title	lobby
client number	A-4.2

moka studio

design and build

rear view



front view



rear view



front view



contractors must check all dimensions on site before starting any work or shop drawings. figured dimensions to take precedence over scale readings.

this drawing is copyright and property of the architects

project title	checked	category	scale	drawing title
apartment	moka	development drawing	A3 - nts	3d view-exterior
client		revision	date	drawing number
mr. paul			25 january 2021	

moka studio

design and build

lobby - first floor



lobby - second floor



building a - first floor



building a - second floor




contractors must check all dimensions on site before starting any work or shop drawings. figured dimensions to take precedence over scale readings.

this drawing is copyright and property of the architects

project title	checked	category	development drawing	scale	A3 - nts	drawing title	3d view-interior	drawing number	
client	moka	revision		date		date		date	
mr . paul				25	january 2021				

rear elevation

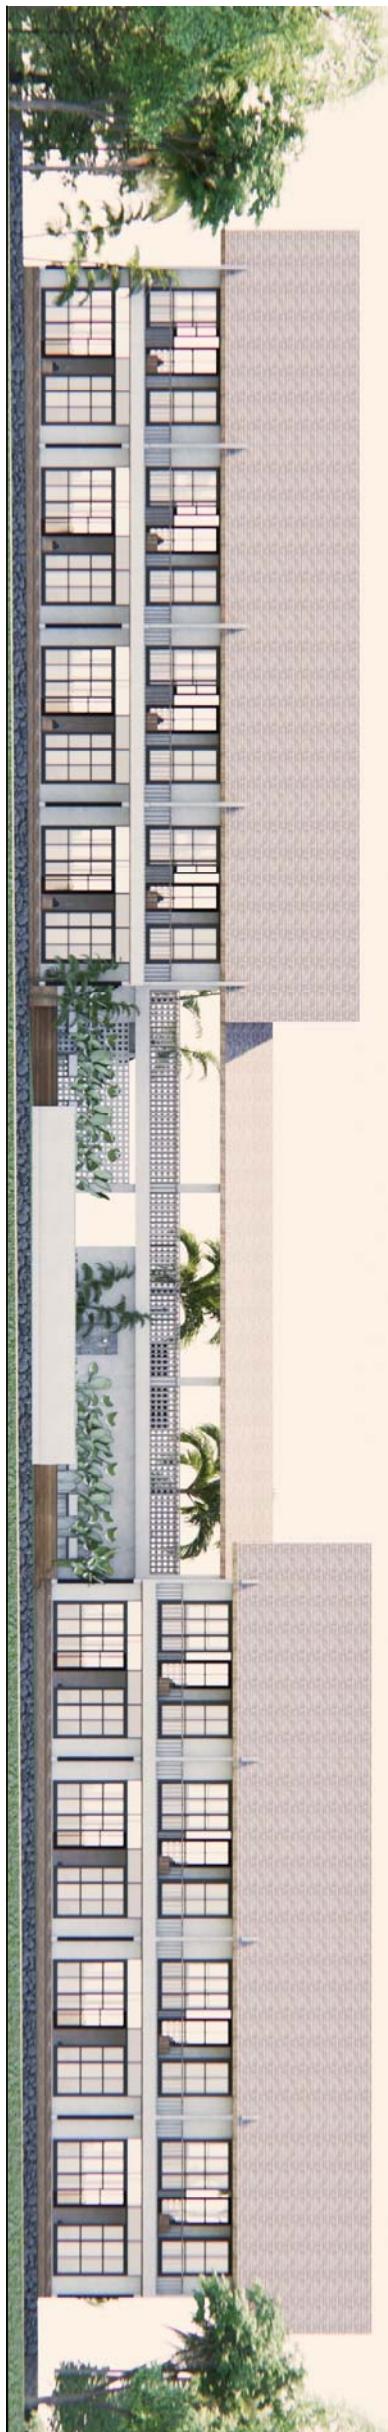

front elevation



moka studio

design and build

project title	checked	category	development drawing	scale	drawing title
apartment	moka			A3 - nts	3d view-elevation
client					
mr. paul					
checked					
dimensions on site before starting any work or shop drawings.					
figured dimensions to take precedence over scale readings.					
this drawing is copyright and property of the architects					